



TH Architecture

972-542214335+ : 70

Client

Shai alfasi Matan morali

Project

k-pn restaurant

No


1


Scale

1 : 50

Date

03/12/2024 22:32:05

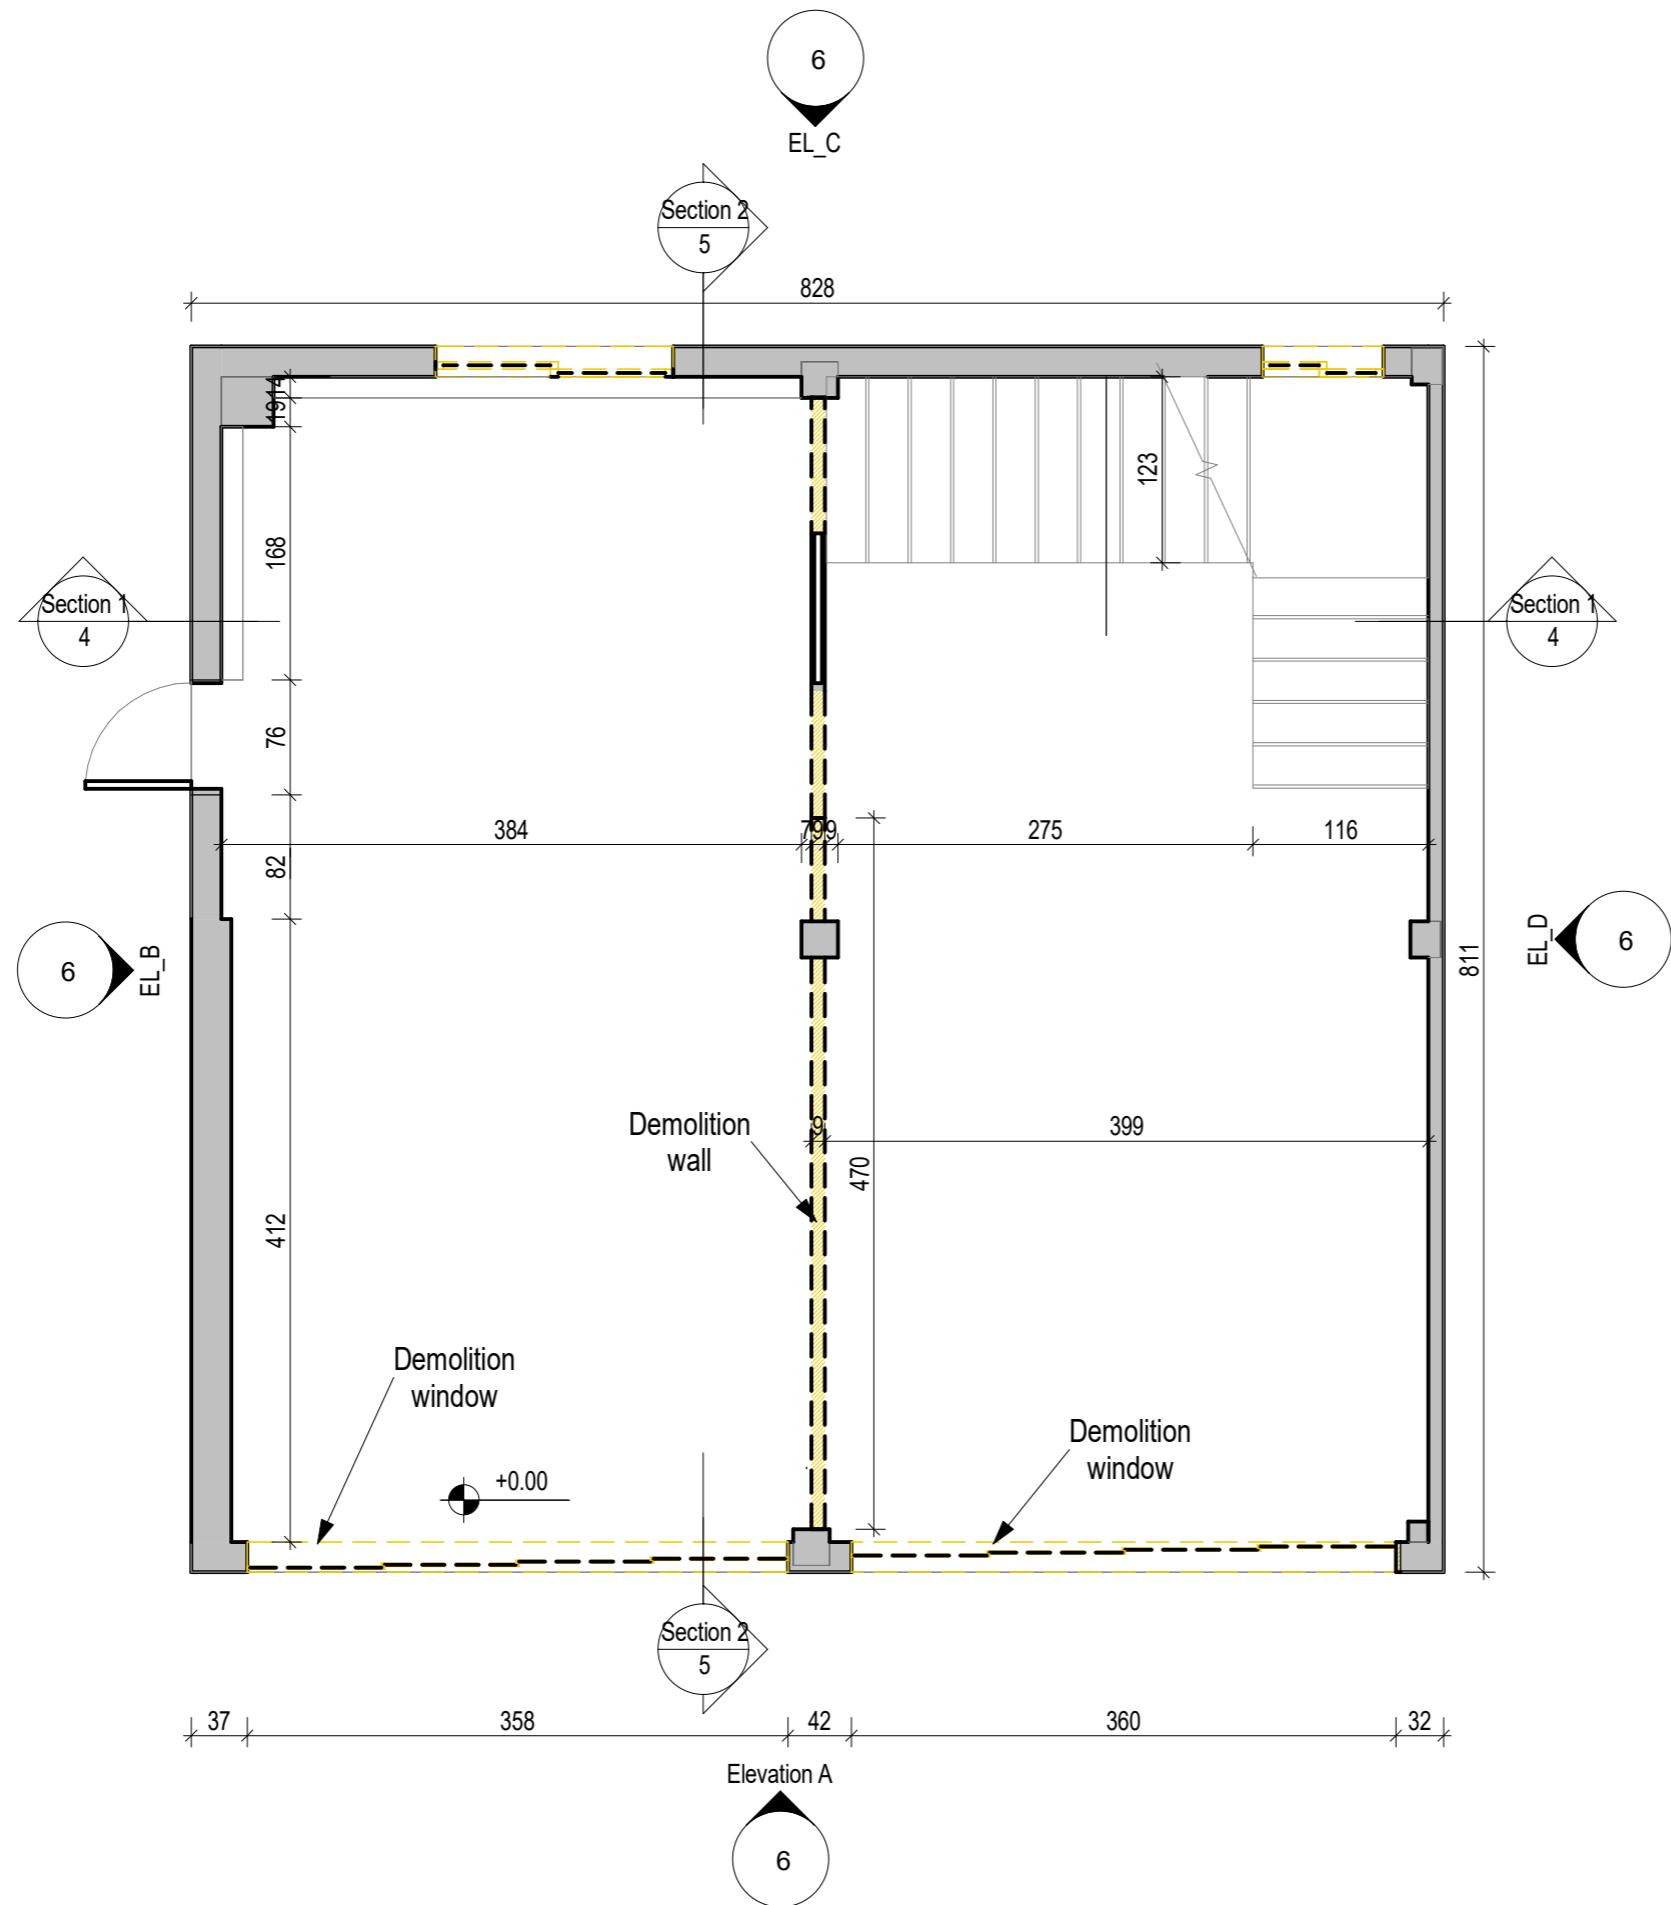

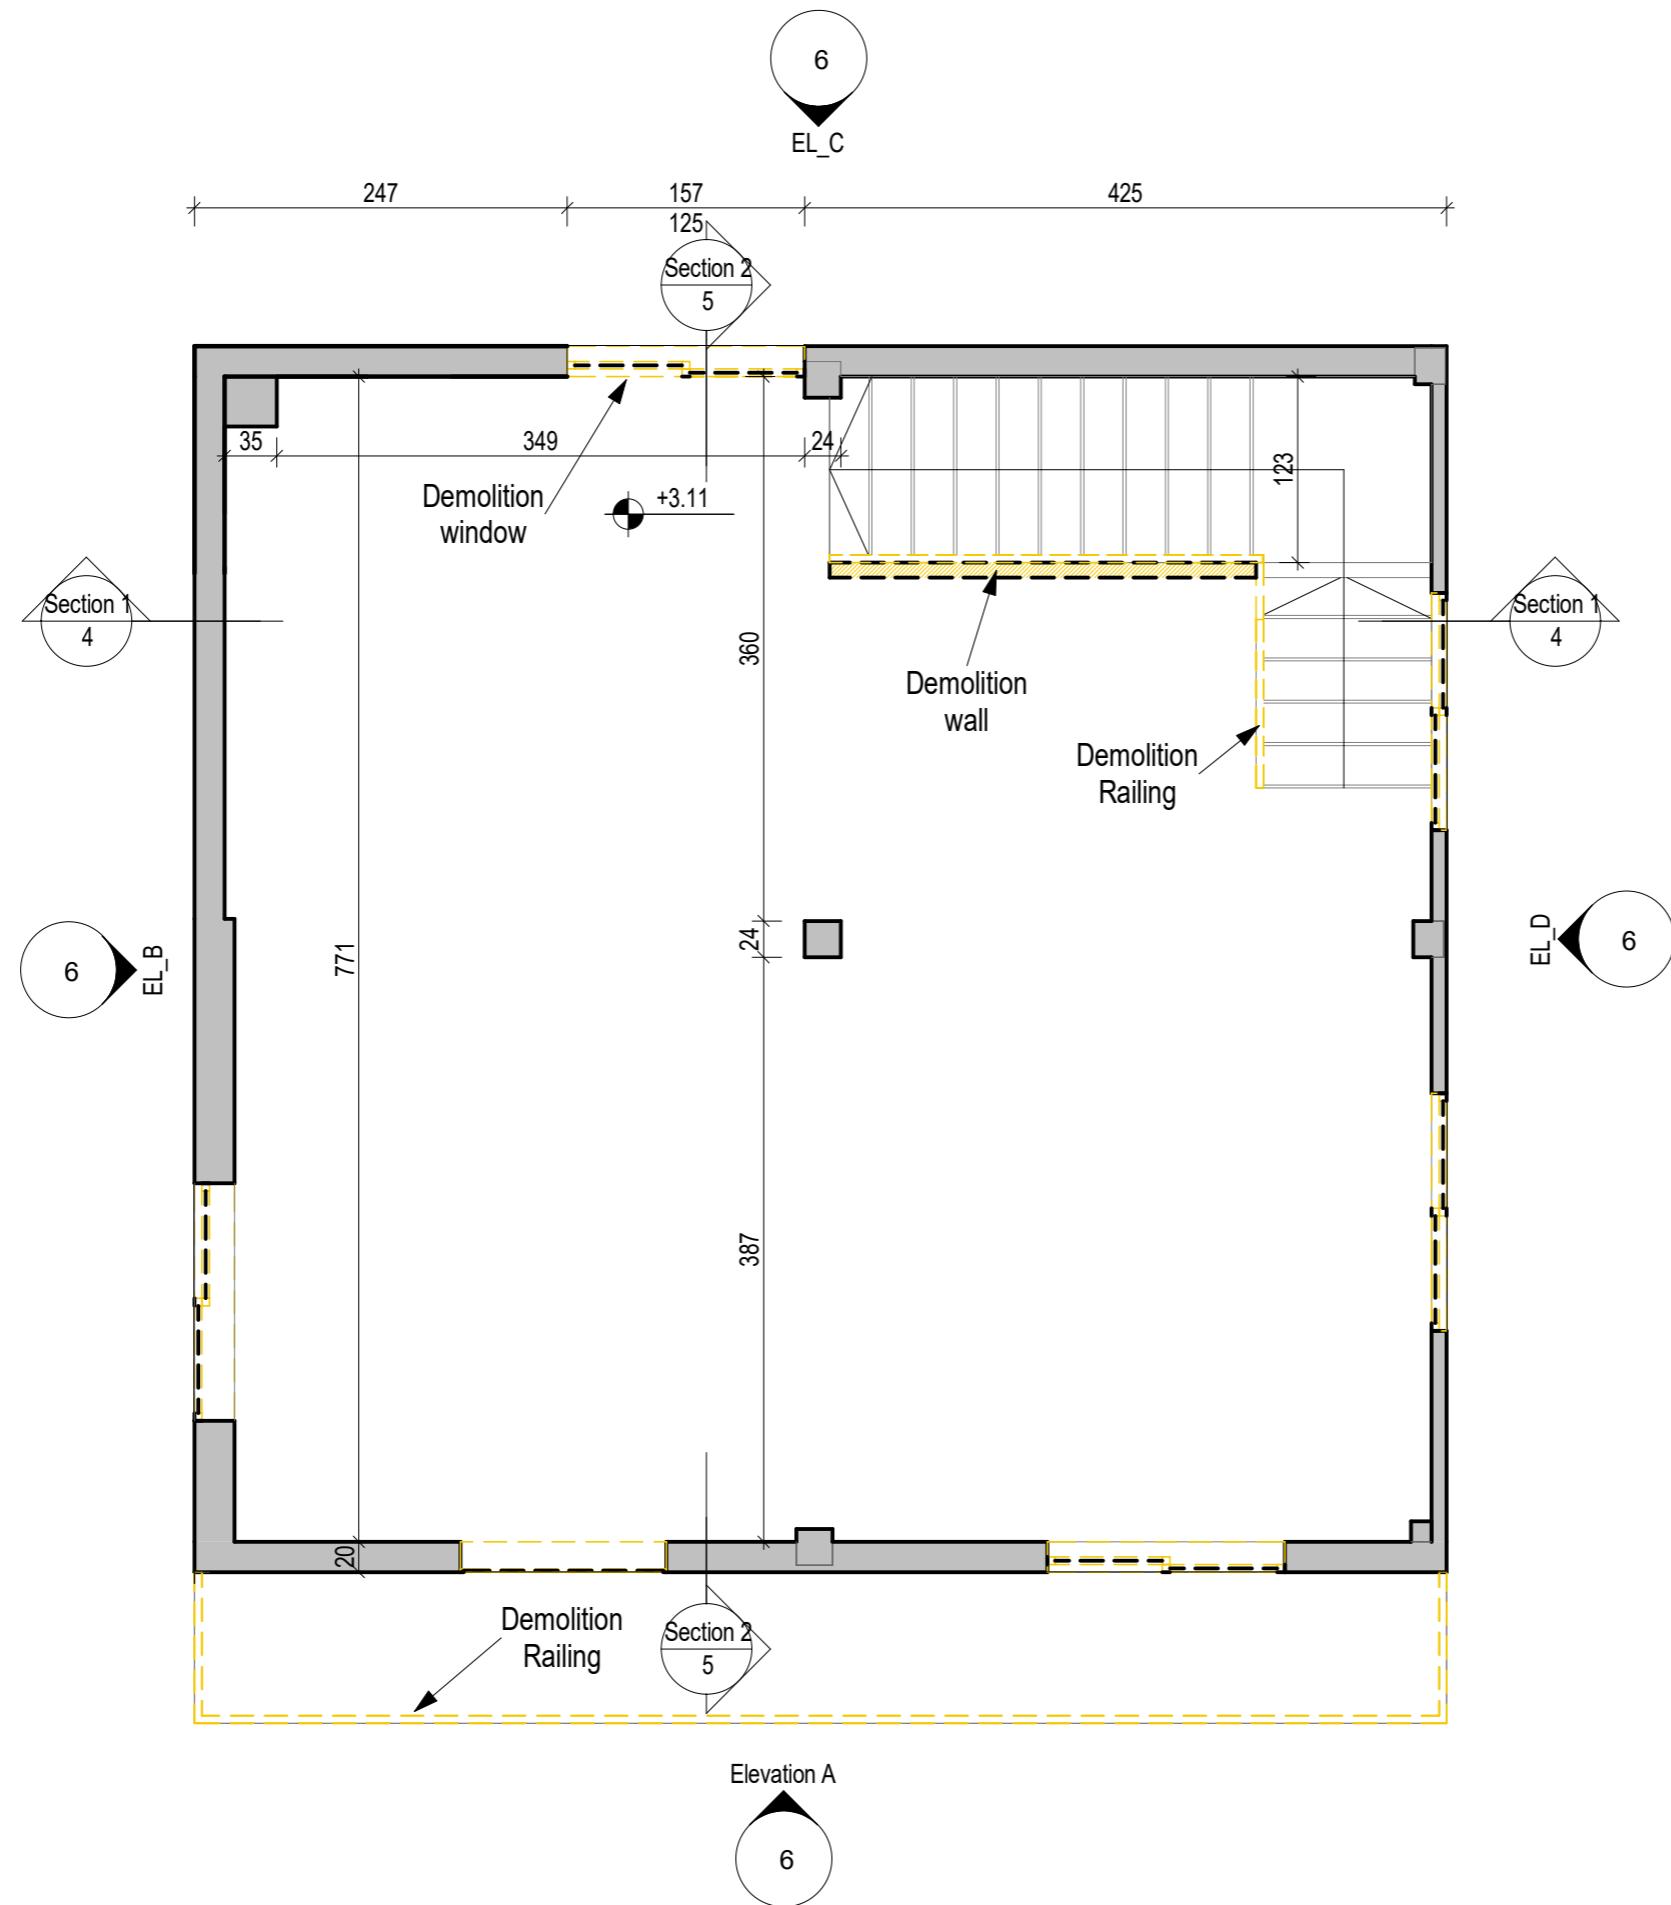
TH Architecture

972-542214335+ : 70

Client

Shai alfasi Matan morali

Project

k-pn restaurant

No


2

Scale

1 : 50

Date

03/12/2024 22:32:06

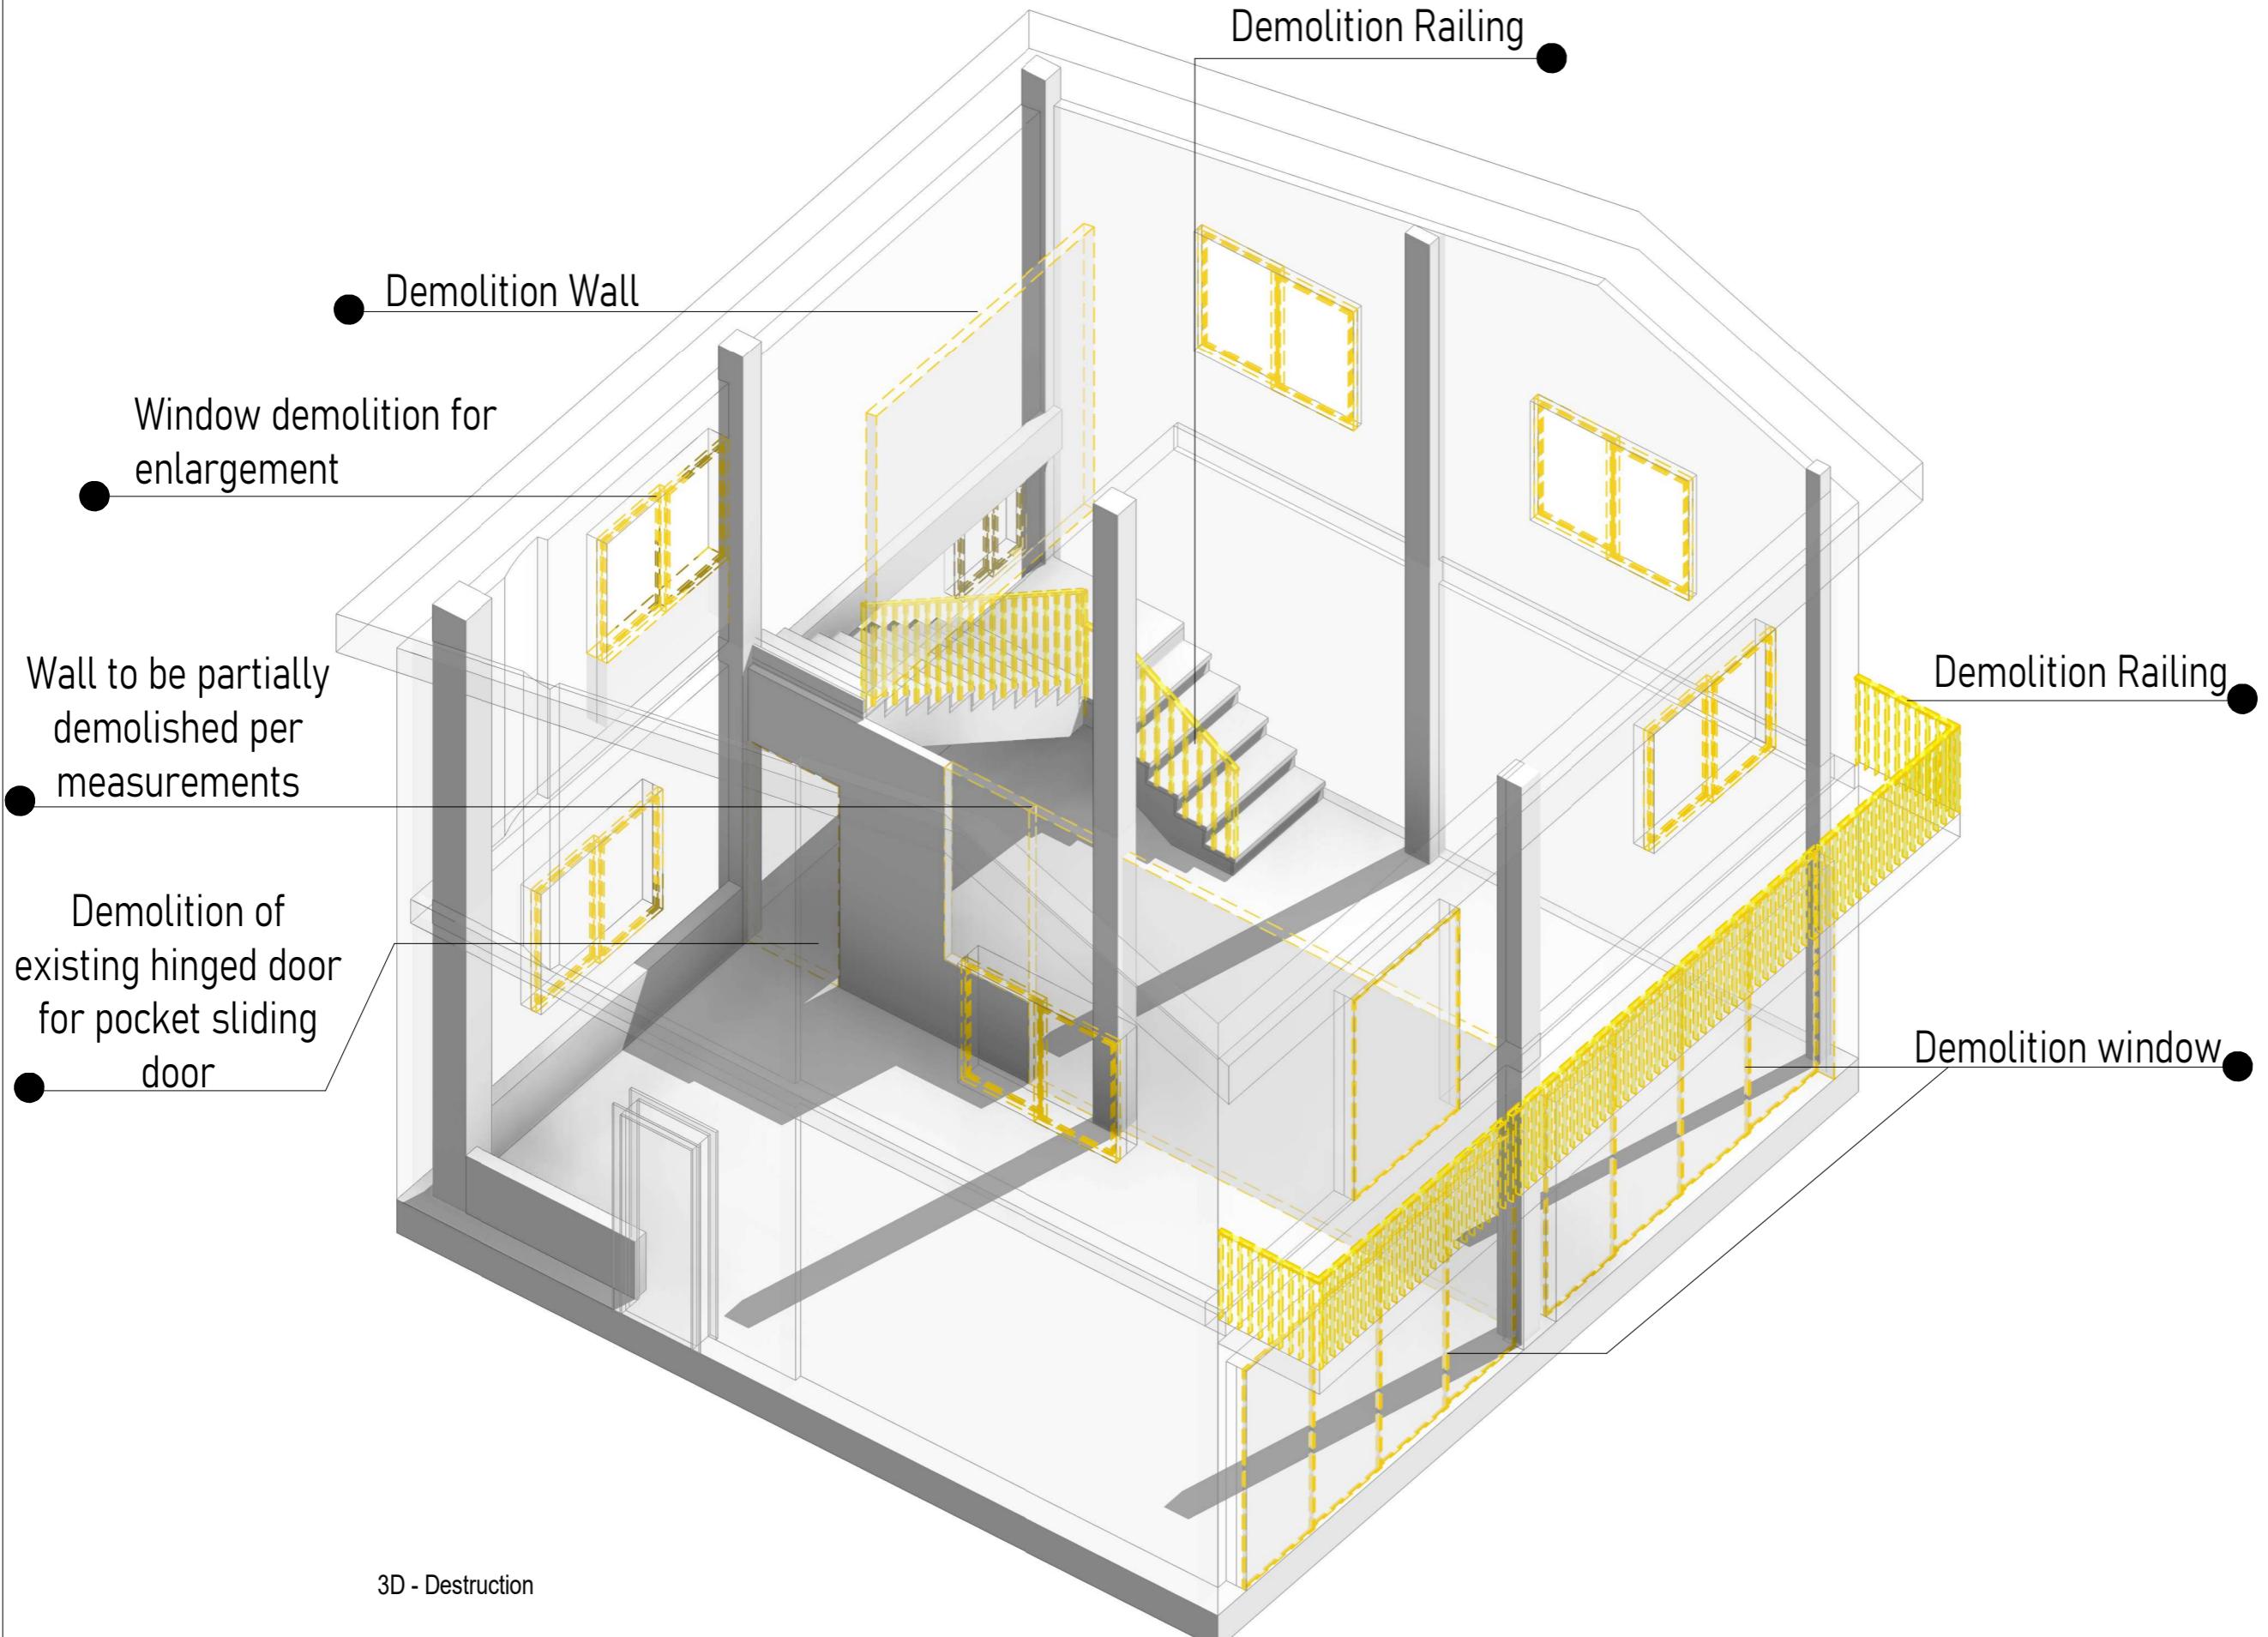

TH Architecture

972-542214335+ : "70

Client

Shai alfasi Matan morali

Project

k-pn restaurant

No


3

Scale

1 : 250

Date

03/12/2024 22:32:07

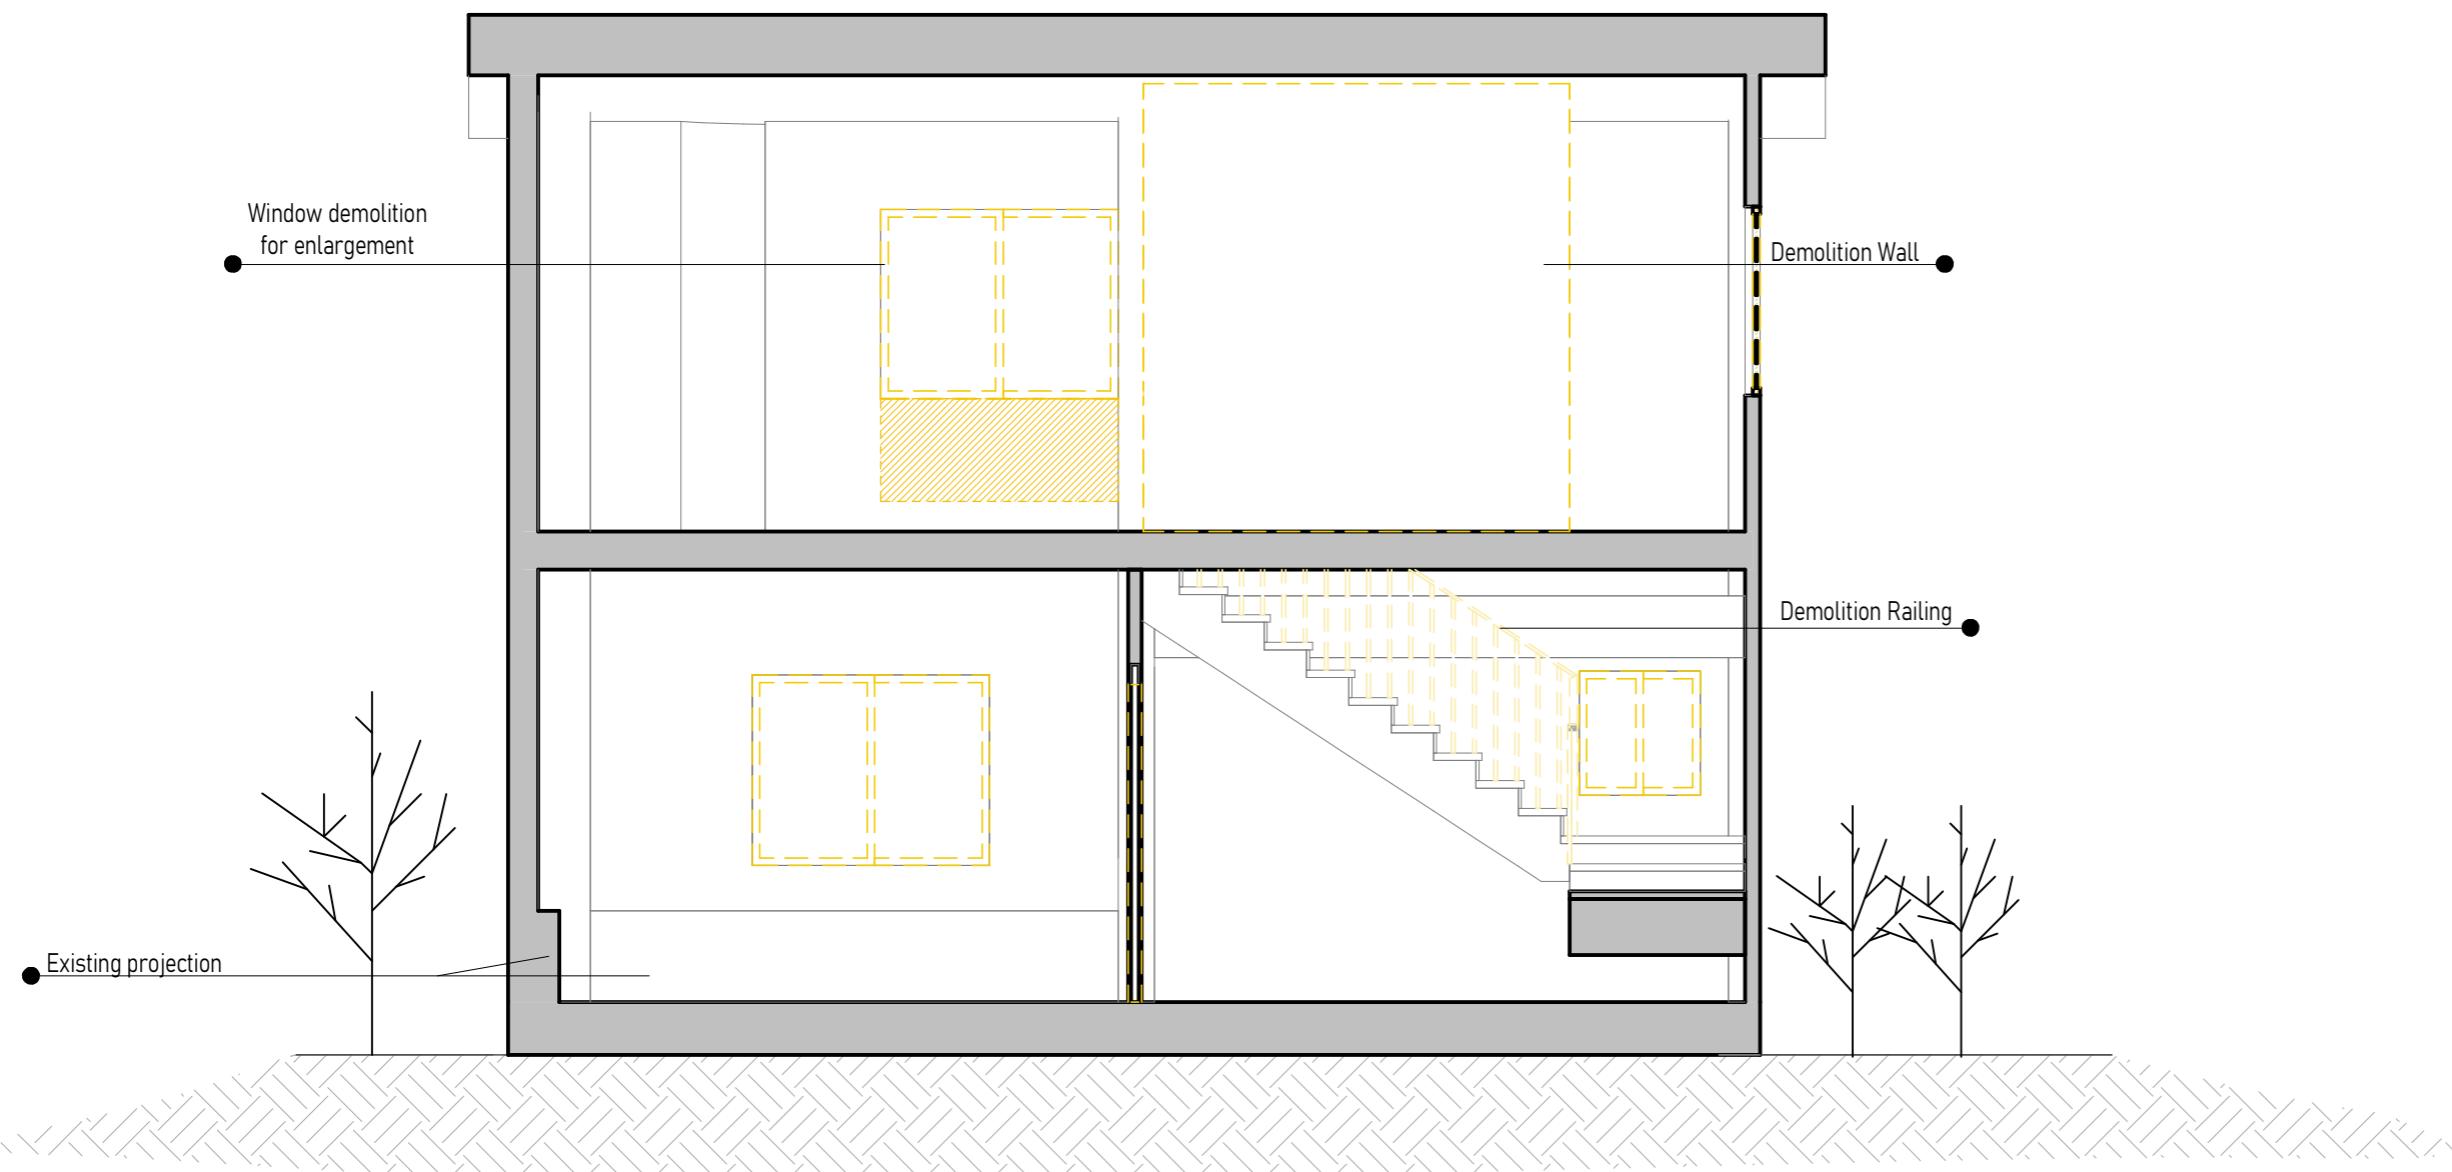

TH Architecture

972-542214335+ : 70

Client

Shai alfasi Matan morali

Project

k-pn restaurant

No


4

Scale

1 : 50

Date

03/12/2024 22:32:08

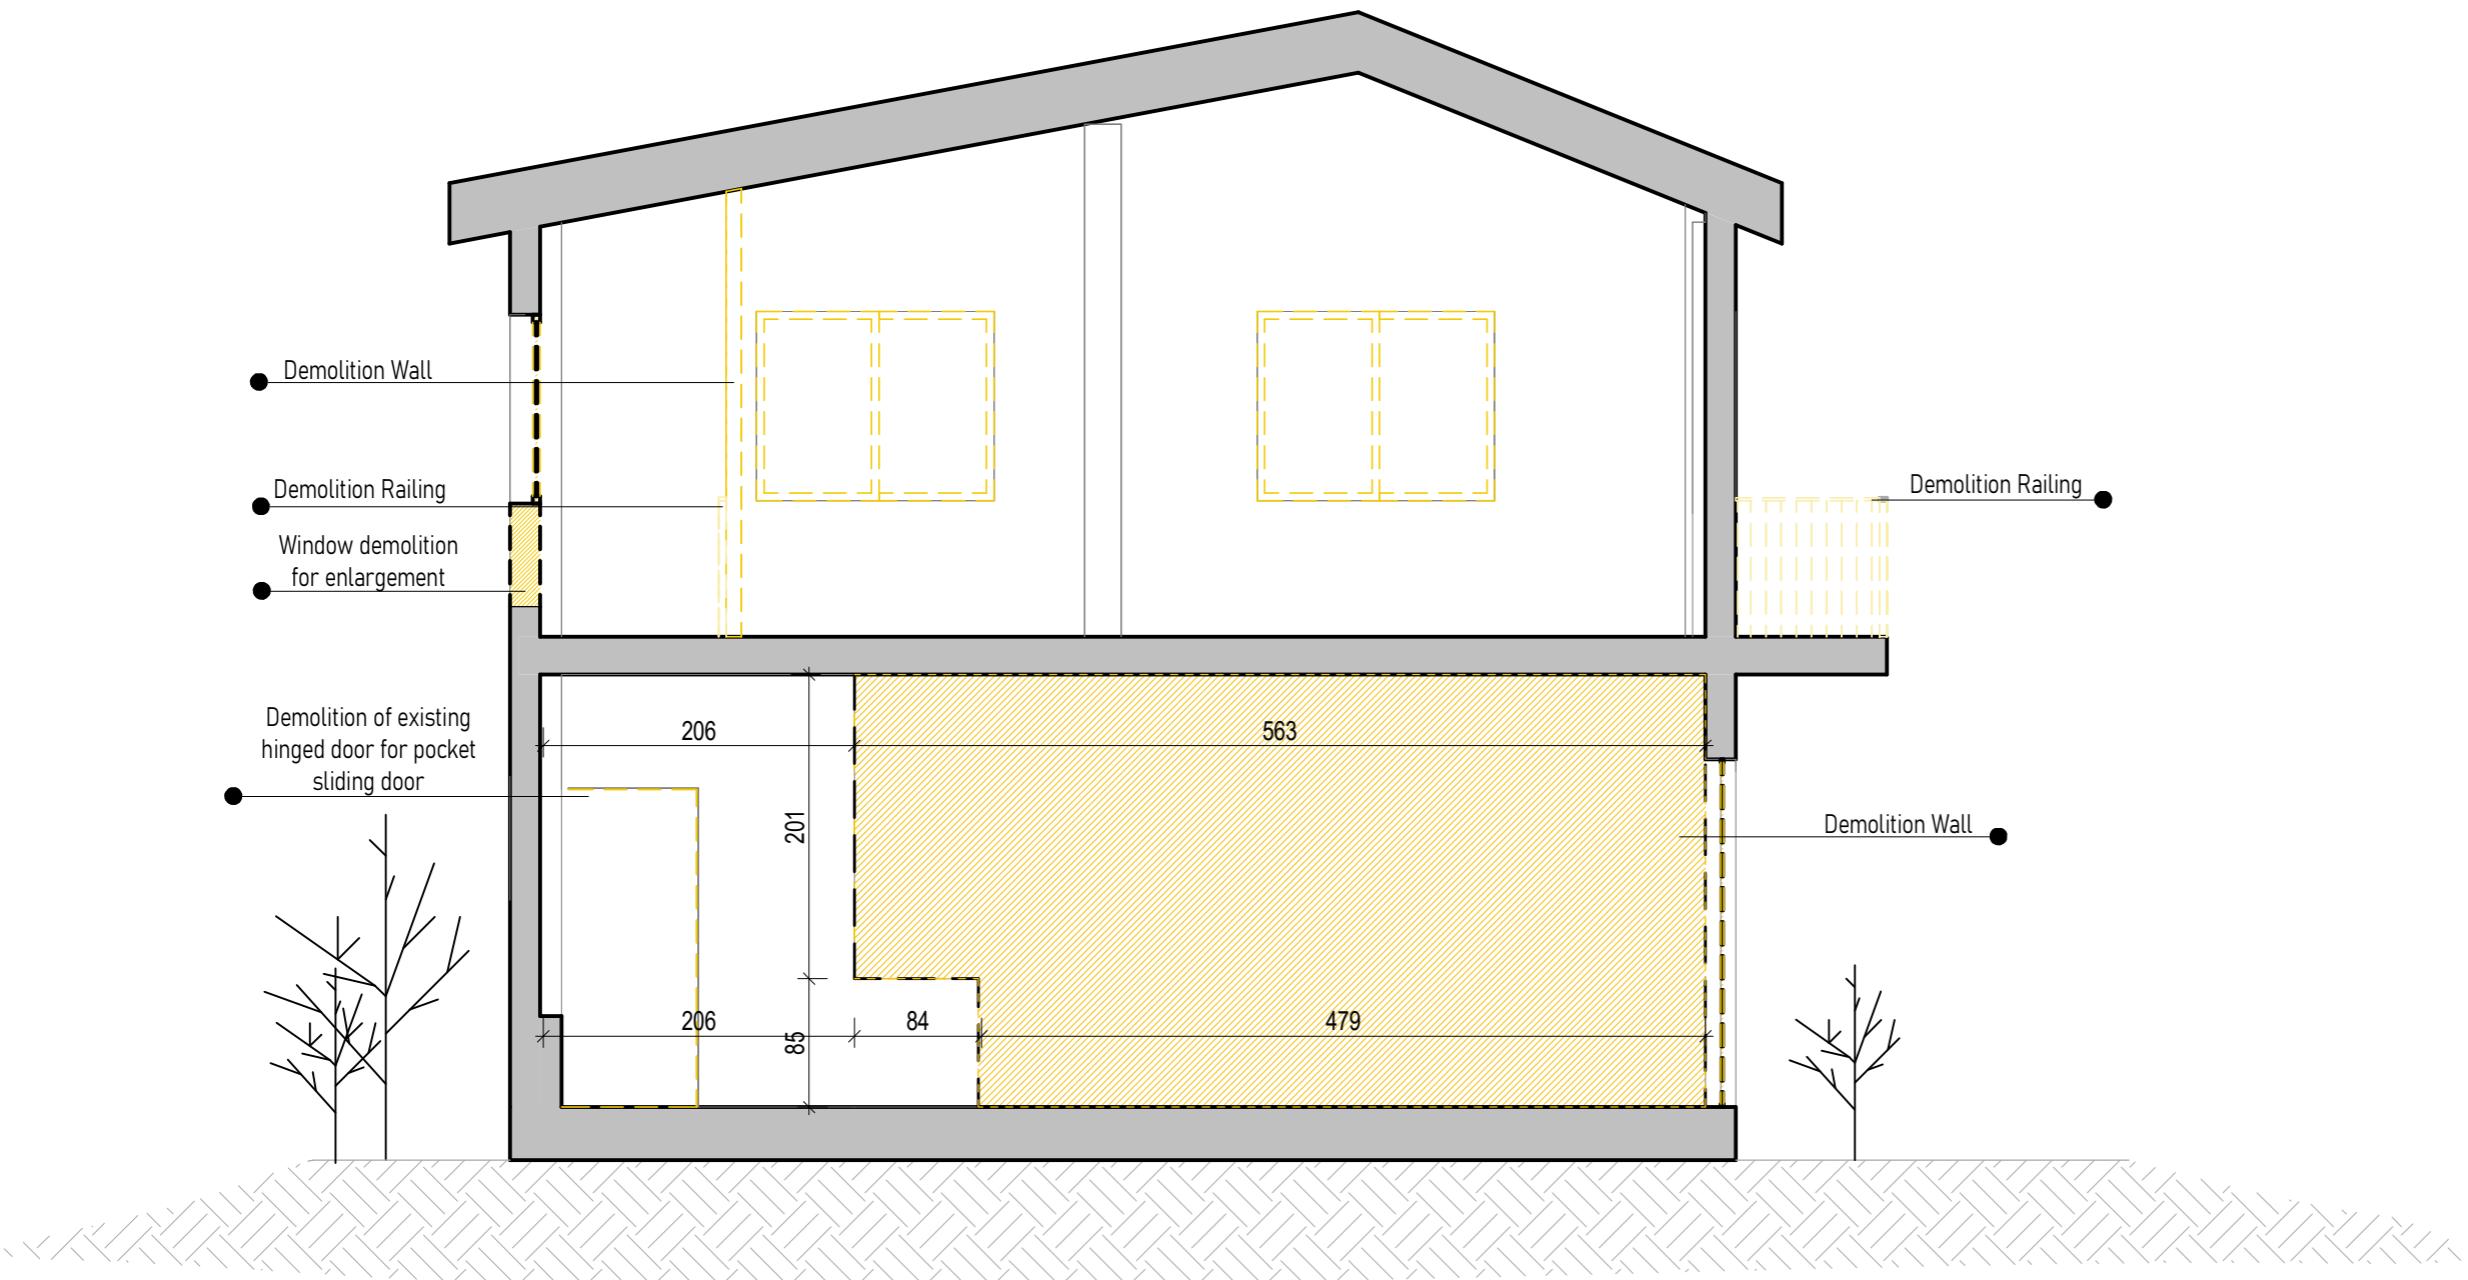

TH Architecture

972-542214335+ : 70

Client

Shai alfasi Matan morali

Project

k-pn restaurant

No

5

Scale


1 : 50

Date


03/12/2024 22:32:08

Destruction Elevations


All windows and showcases will be replaced with Belgian windows after taking precise measurements from the area and according to aluminum lists

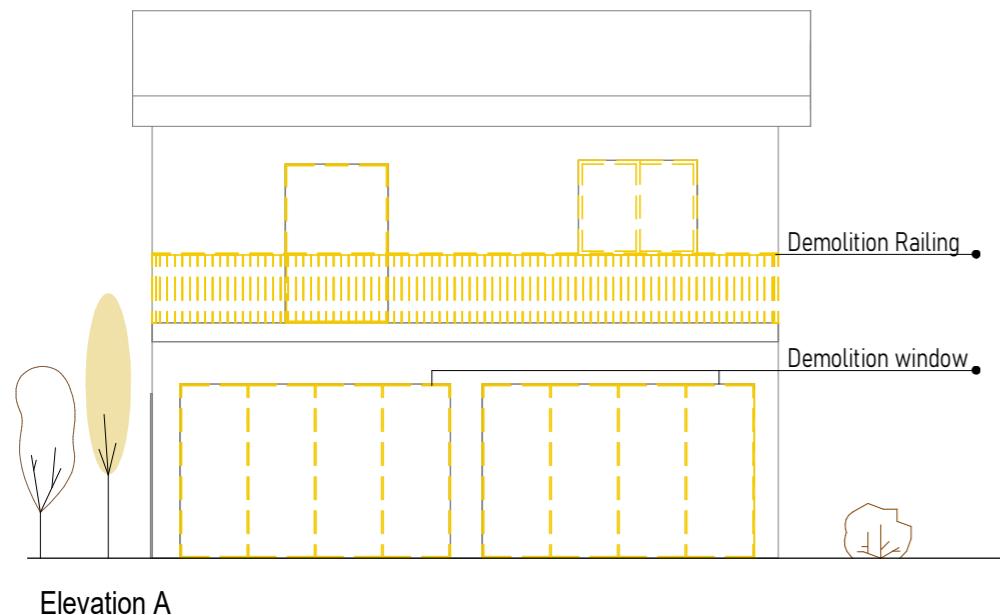


Elevation A

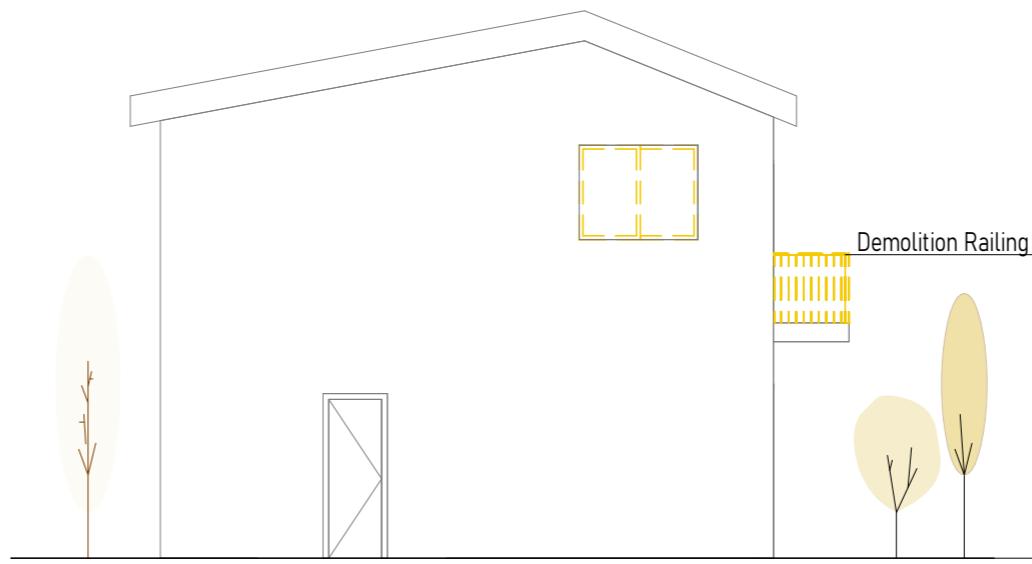

Elevation B

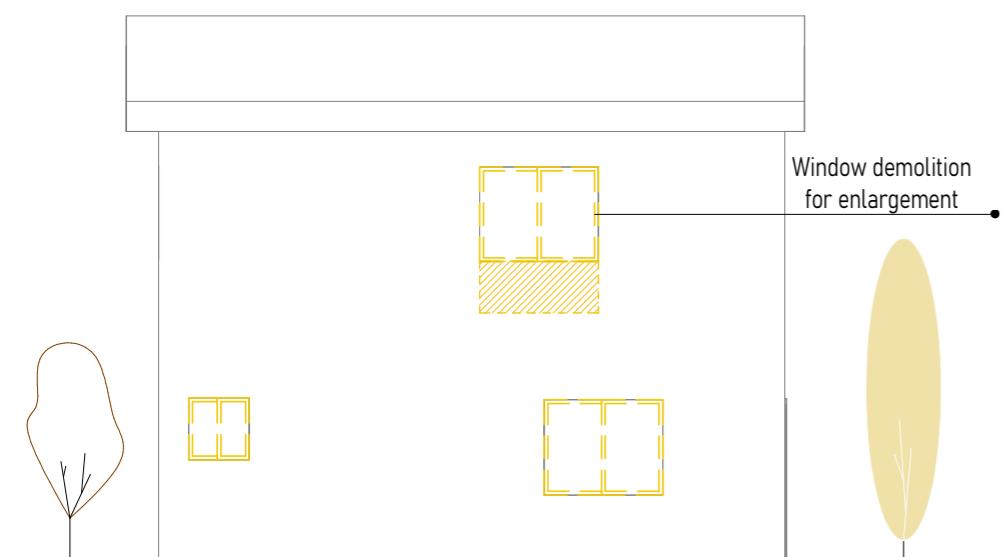

Elevation C

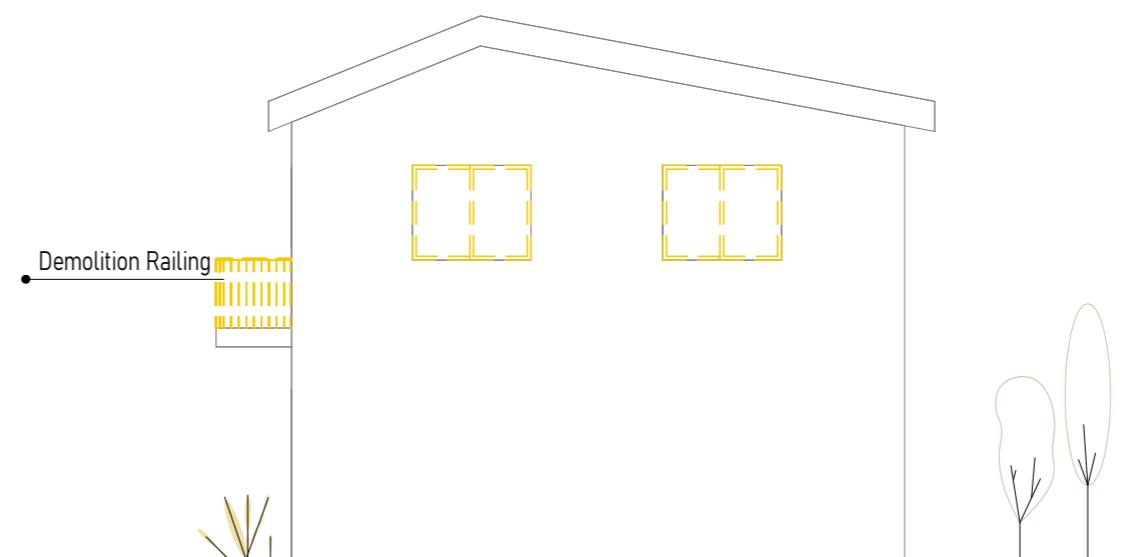

Elevation D



TH Architecture

972-542214335+ :נע

Client

Shai alfasi Matan morali

Project

k-pn restaurant

No


6

Scale

1 : 100

Date

03/12/2024 22:32:09

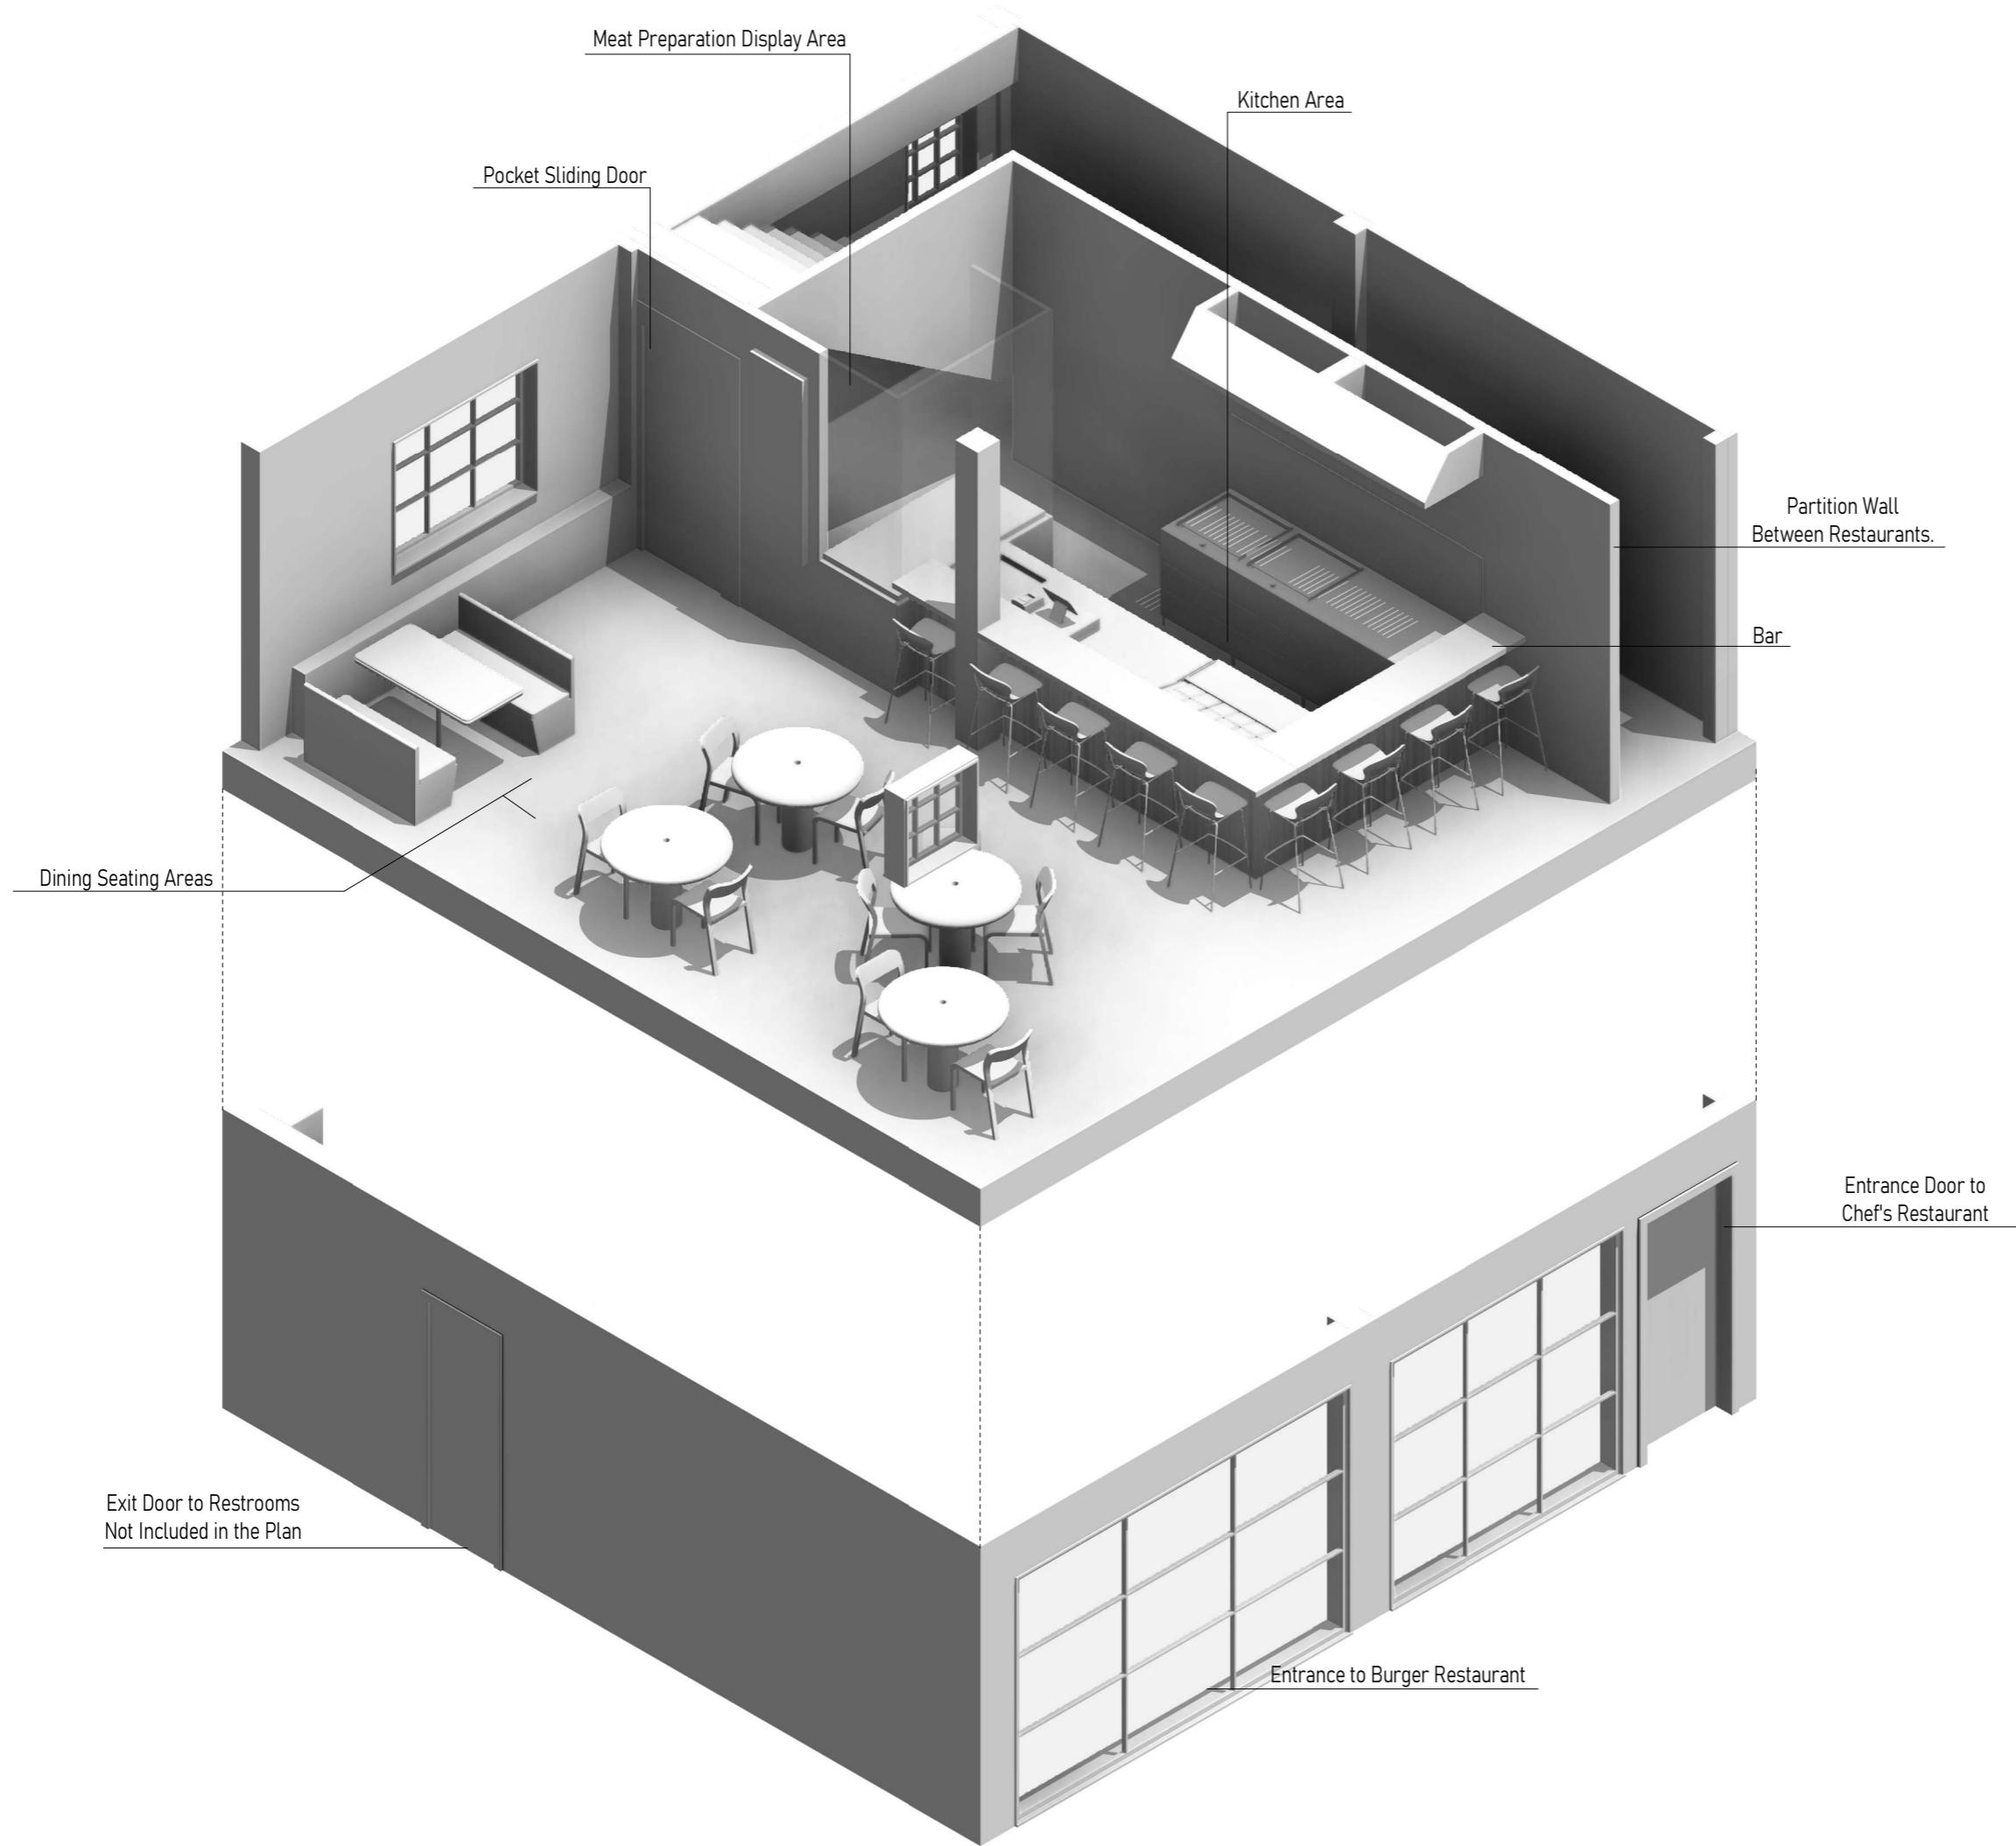**TH Architecture**

972-542214335+ :נע

Client

Shai alfasi Matan morali

Project

k-pn restaurant

No

7

Scale

Date

03/12/2024 22:32:11



TH Architecture

972-542214335+ :70

Client

Shai alfasi Matan morali

Project

k-pn restaurant

No


8

Scale

1 : 50

Date

03/12/2024 22:32:12

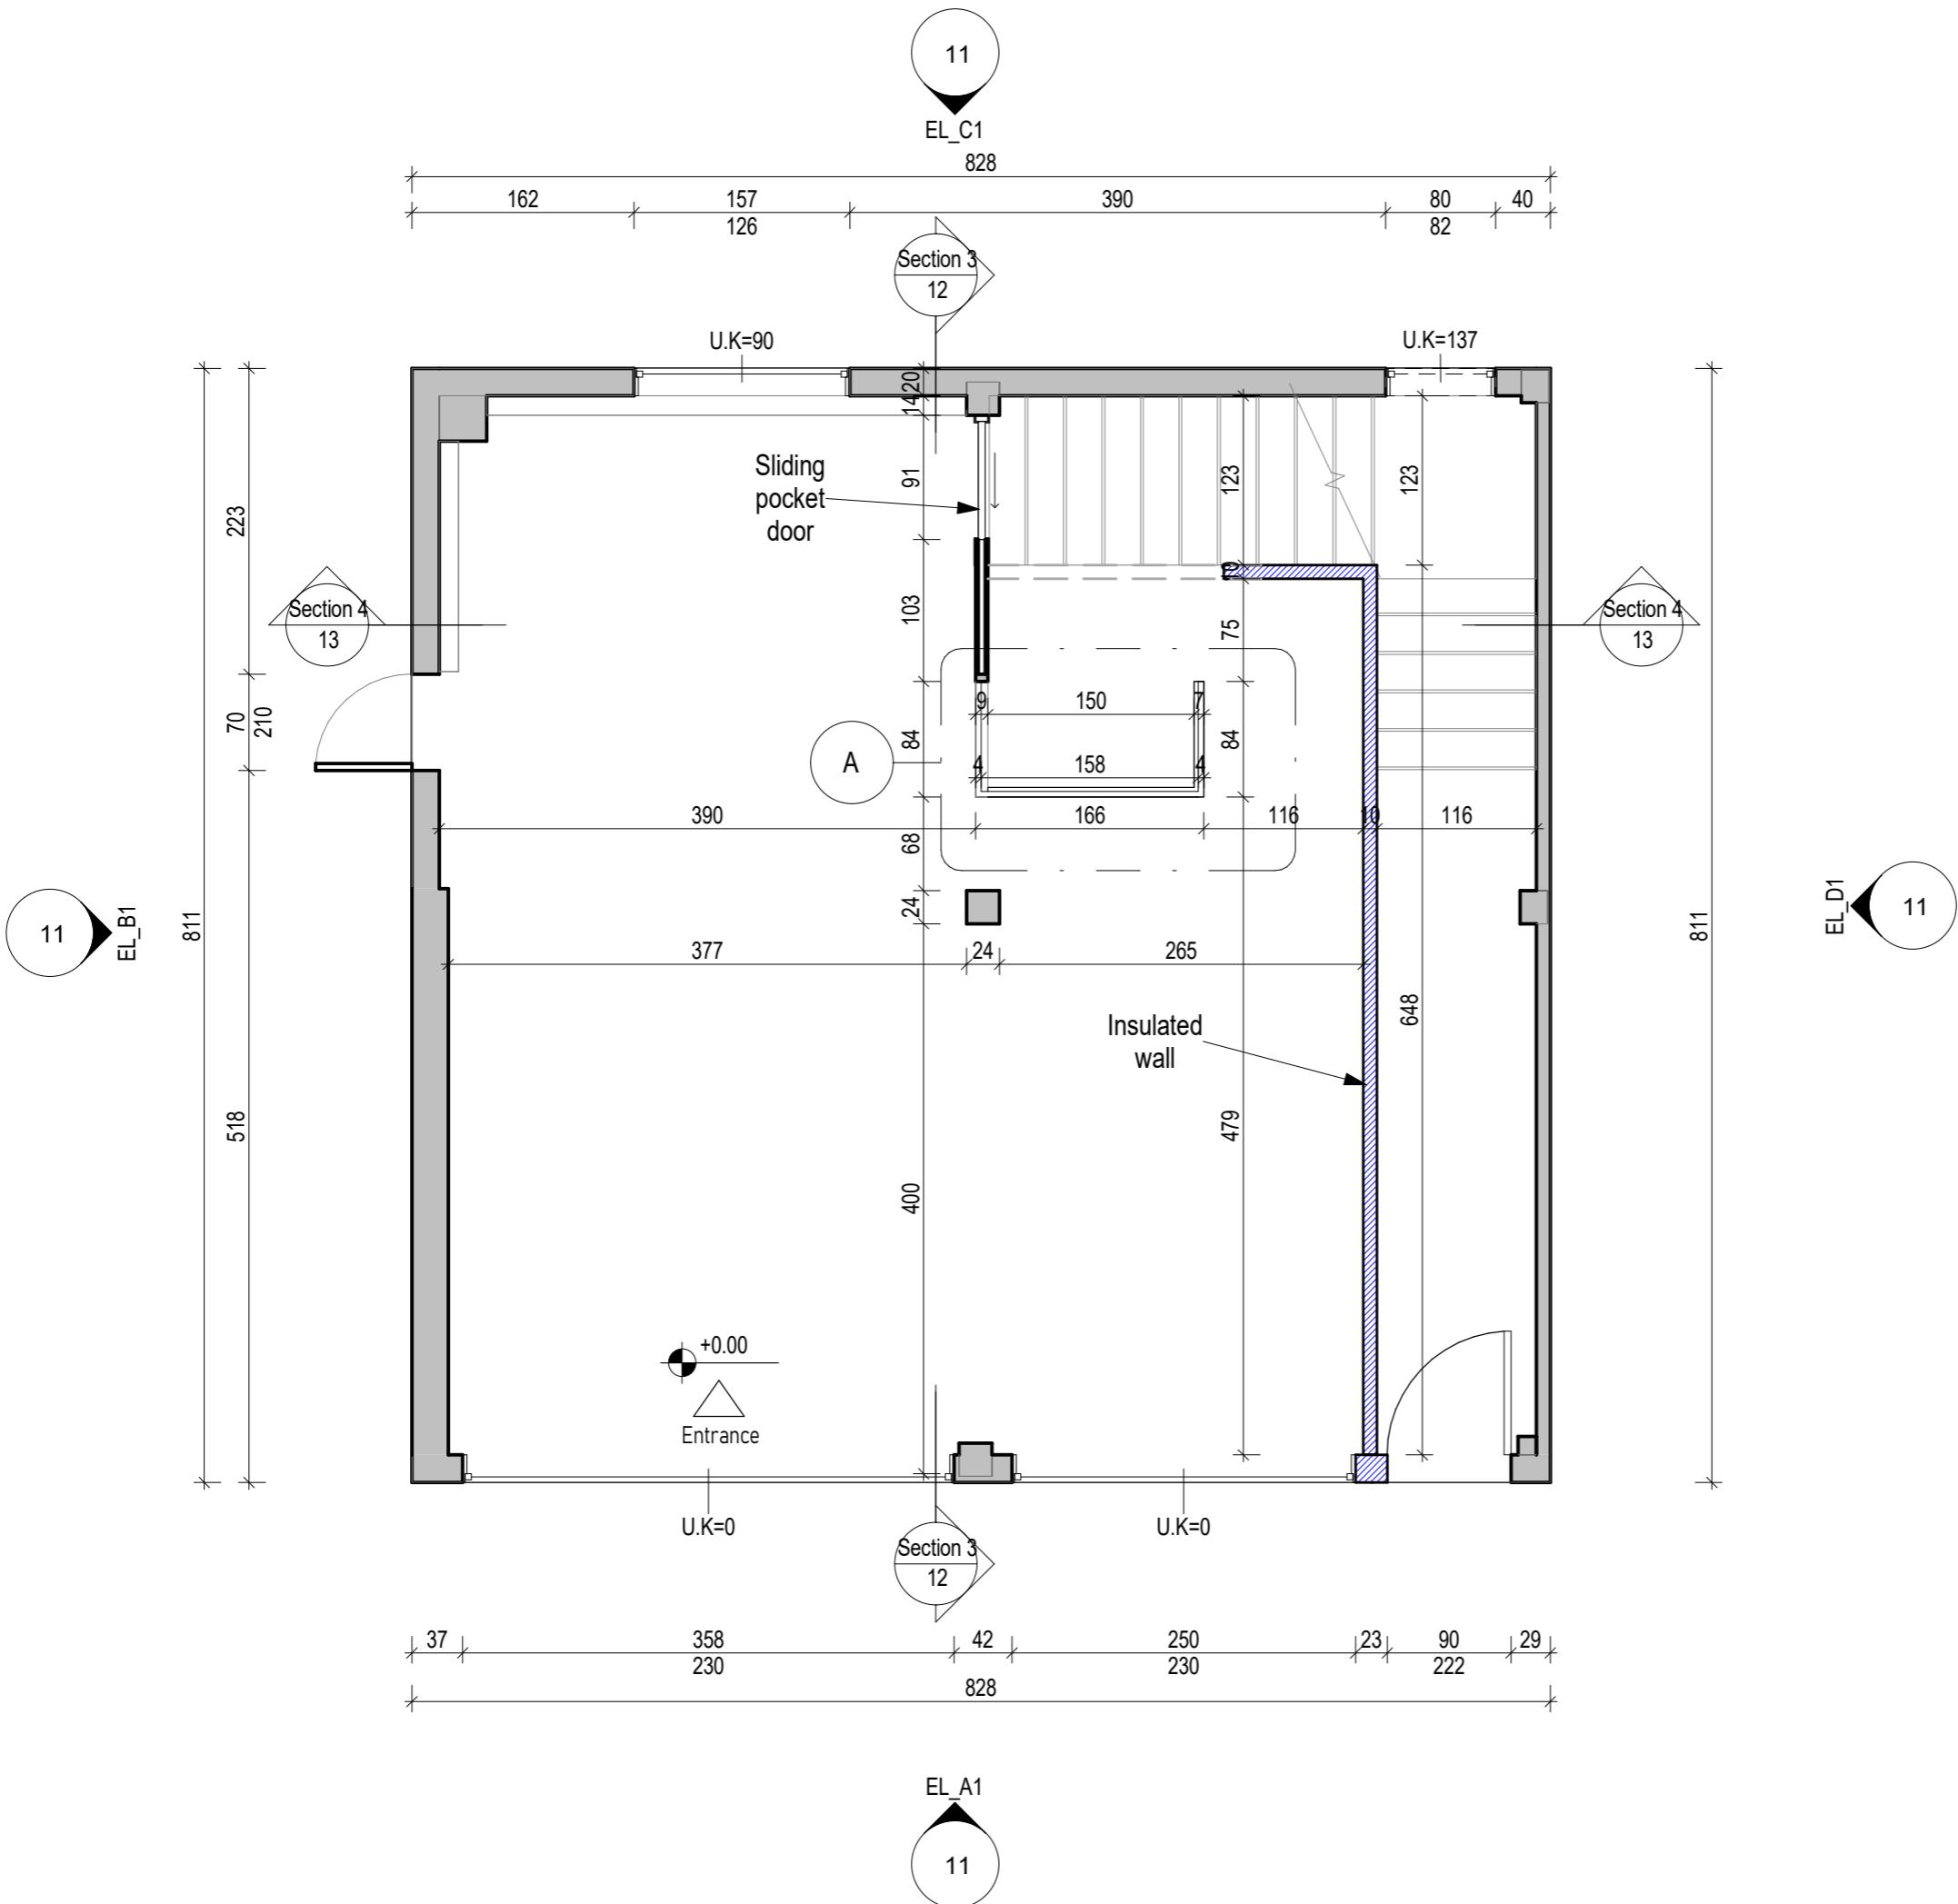



TH Architecture

972-542214335+ : 70

Client

Shai alfasi Matan morali

Project

k-pn restaurant

No



A

Scale

1 : 25


Date

03/12/2024 22:32:19

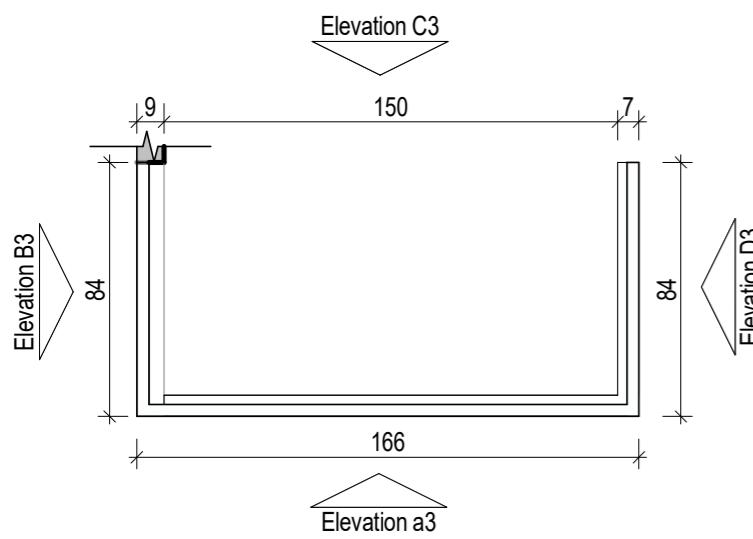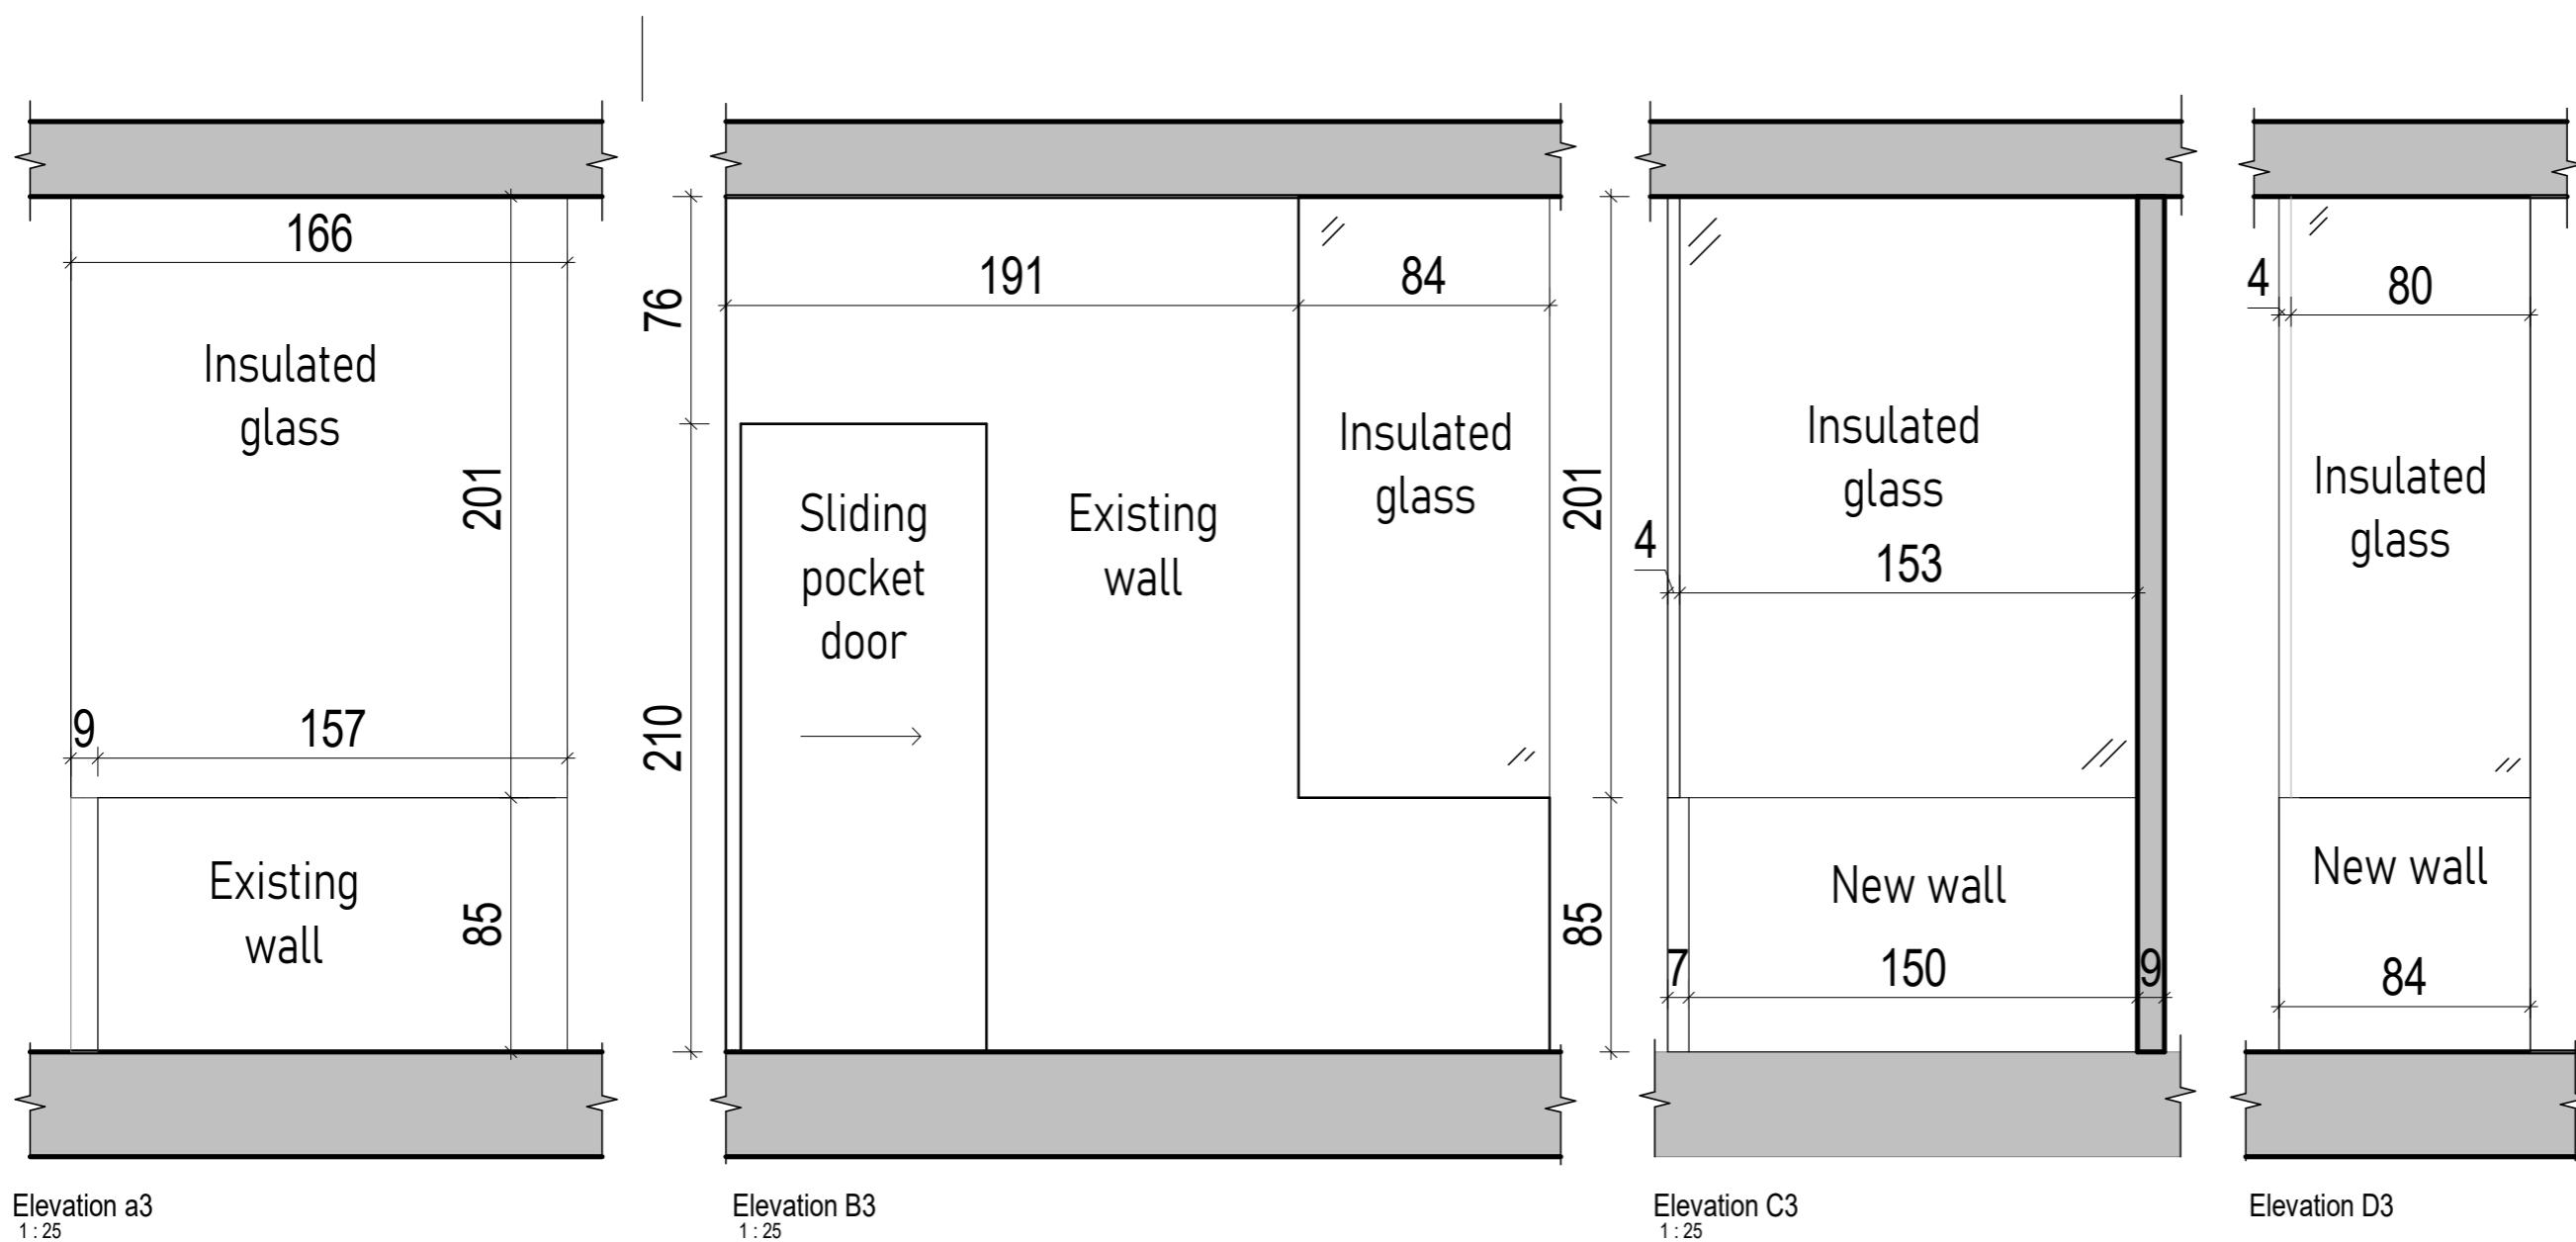


Detail A

3D - Front 1:100

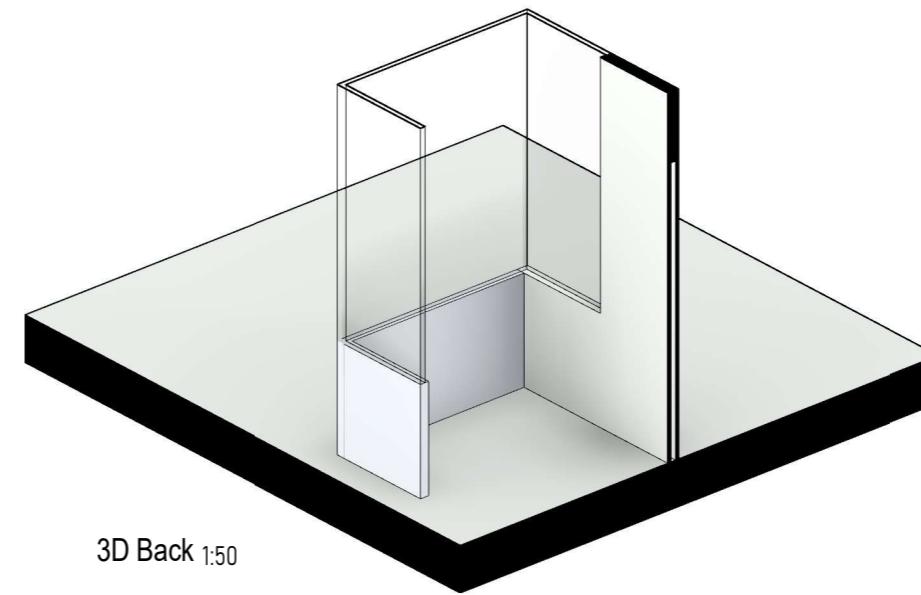

Date

03/12/2024 22:32:19

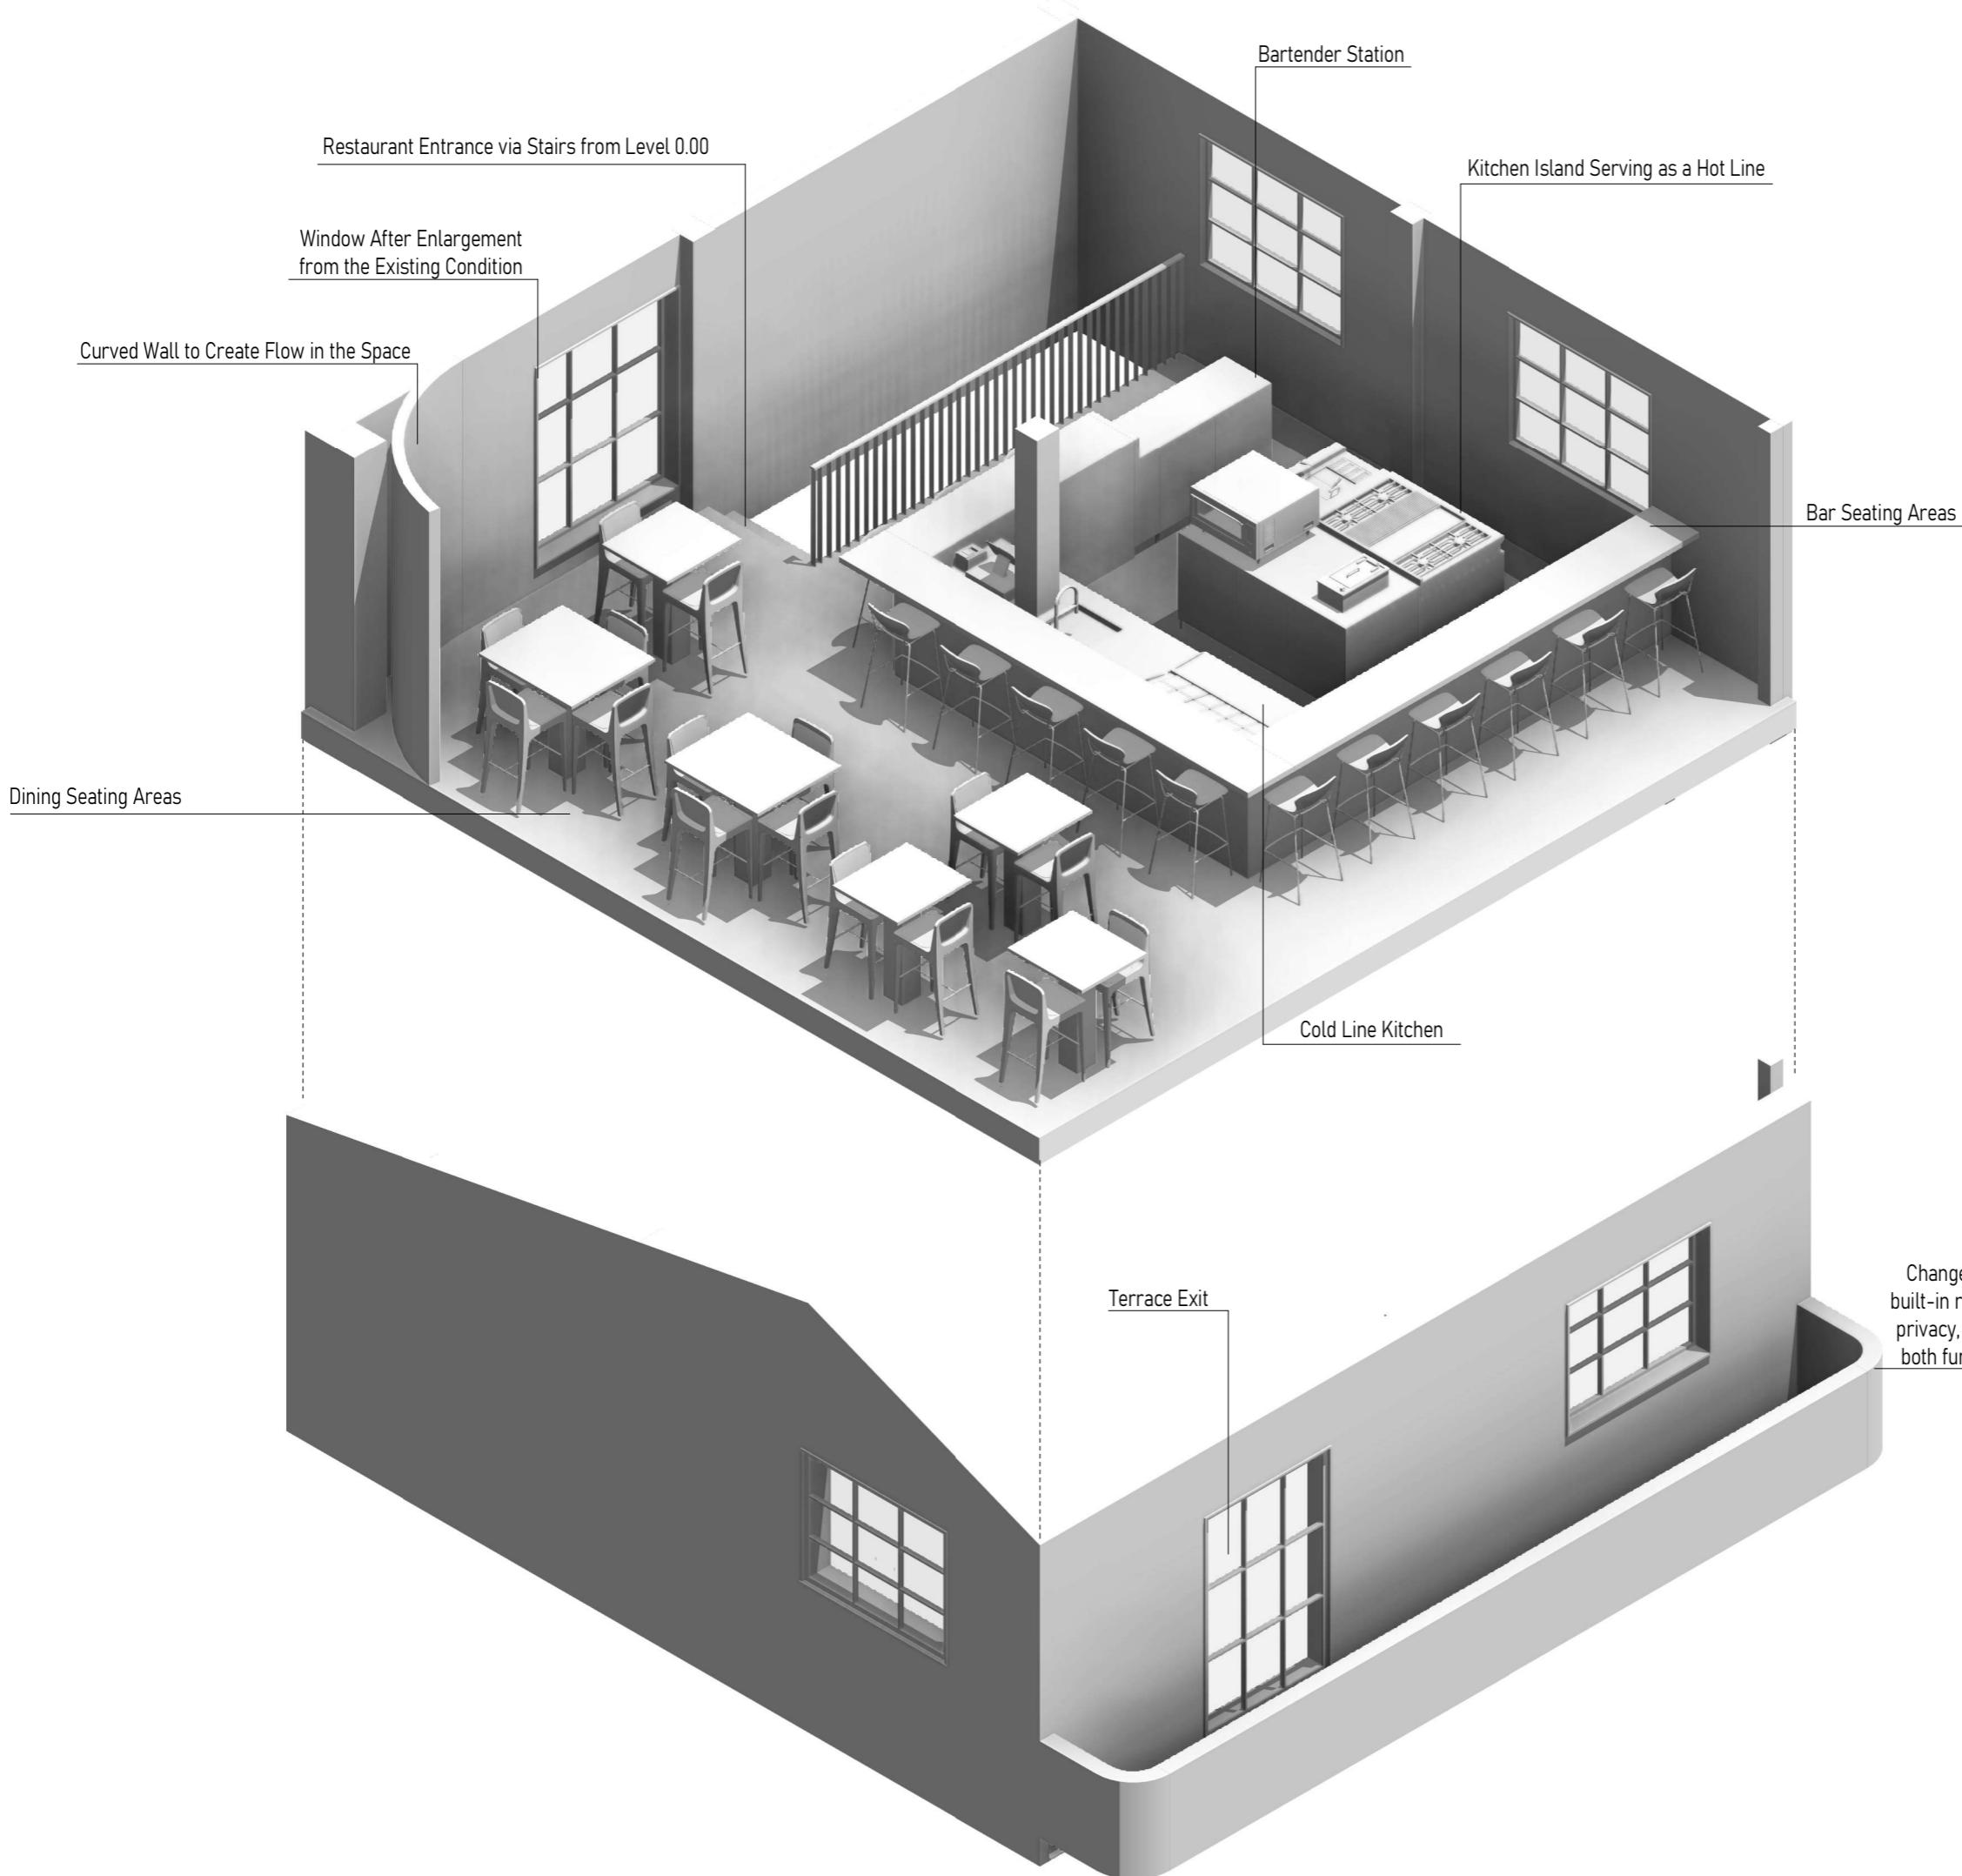

TH Architecture

972-542214335+ :נע

Client

Shai alfasi Matan morali

Project

k-pn restaurant

No

9

Scale

Date

03/12/2024 22:32:23



TH Architecture

972-542214335+ :70

Client

Shai alfasi Matan morali

Project

k-pn restaurant

No


10

Scale

1 : 50

Date

03/12/2024 22:32:24

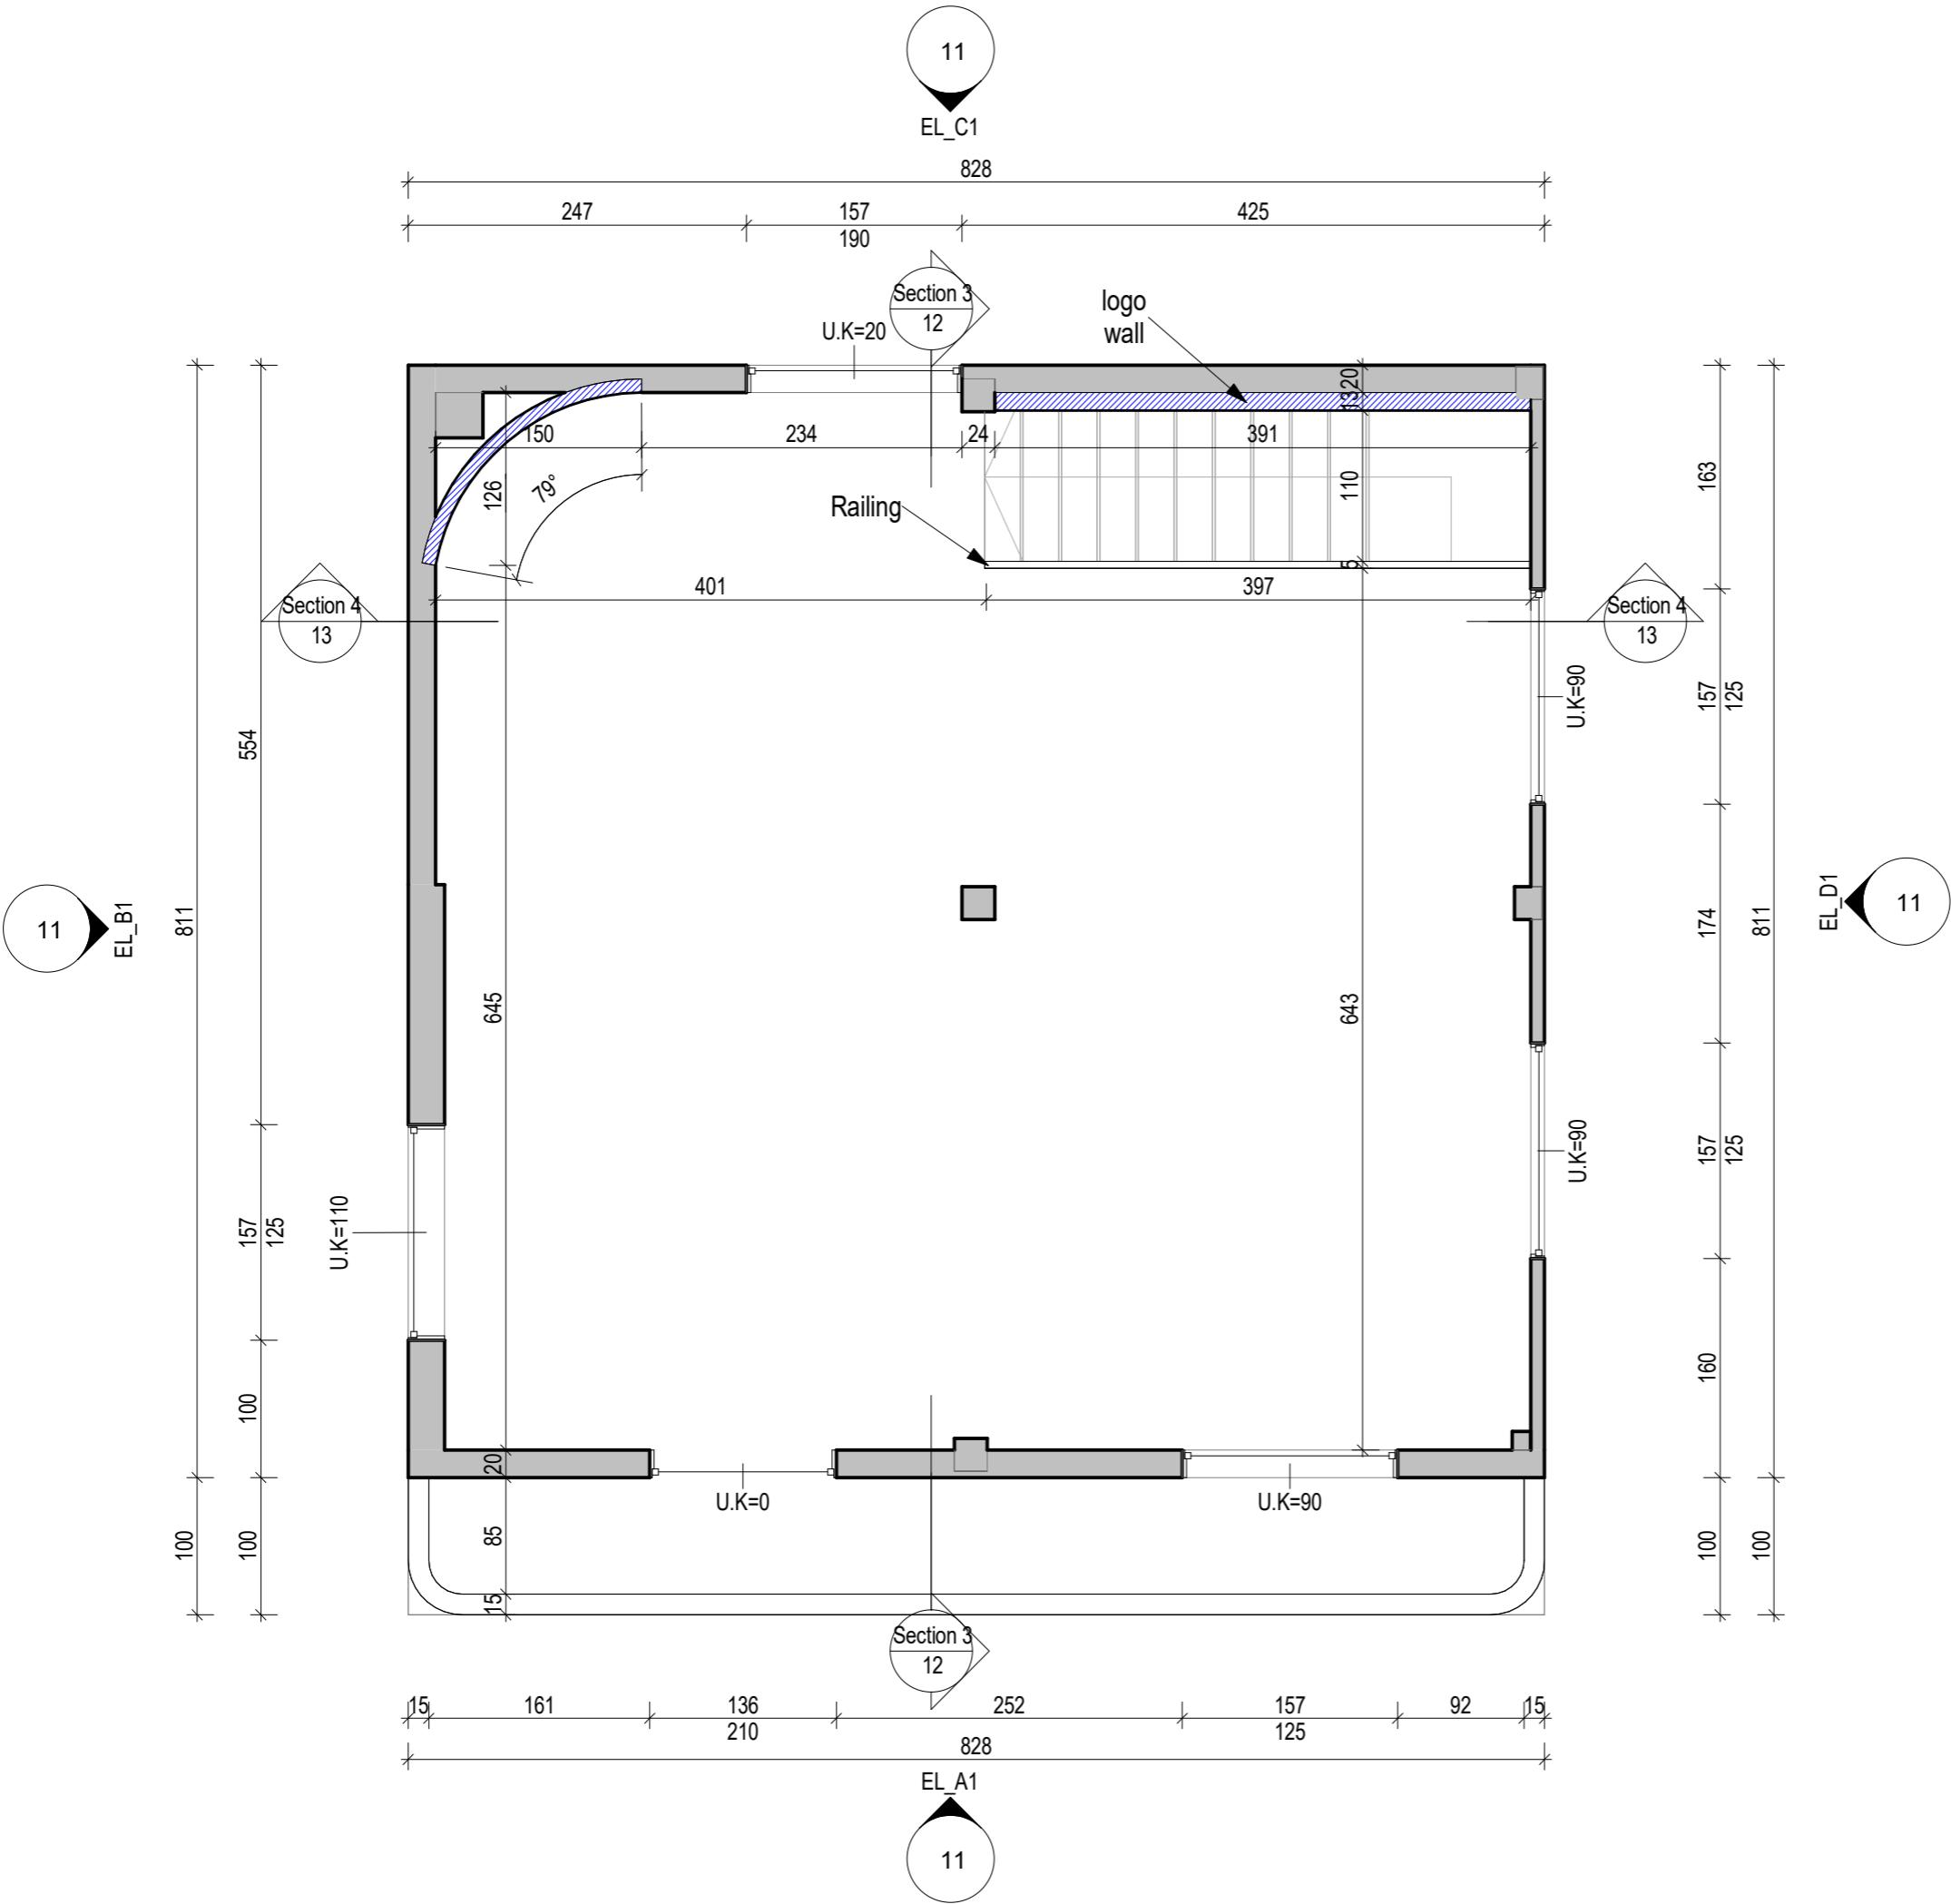

All windows and showcases will be replaced with Belgian windows after taking precise measurements from the area and according to aluminum lists



TH Architecture

972-542214335+ : 70

Client

Shai alfasi Matan morali

Project

k-pn restaurant

No





11


Scale

1 : 100

Date

03/12/2024 22:32:26

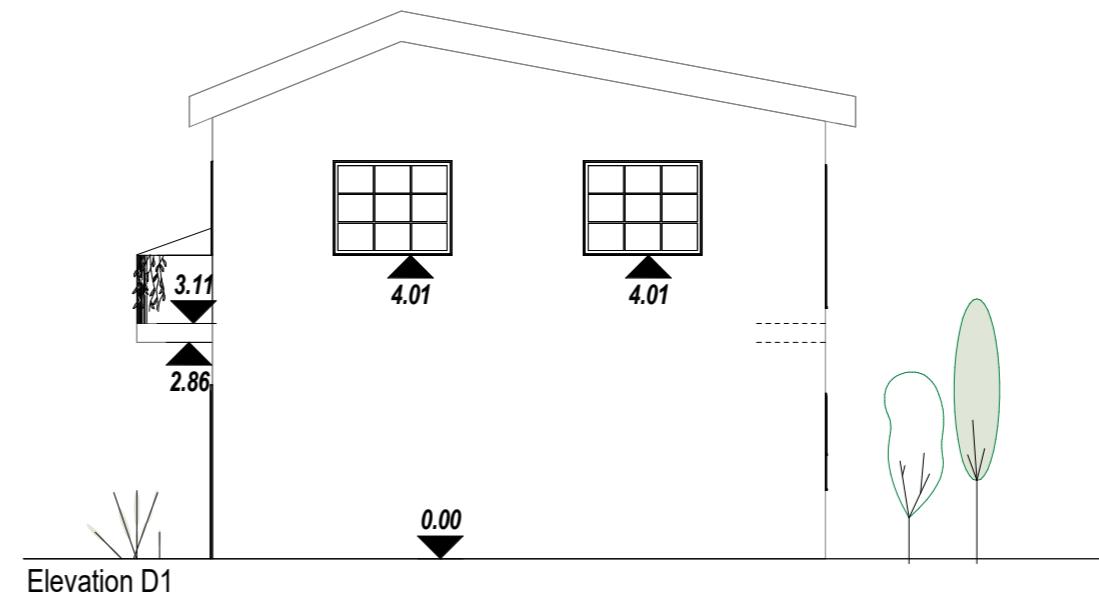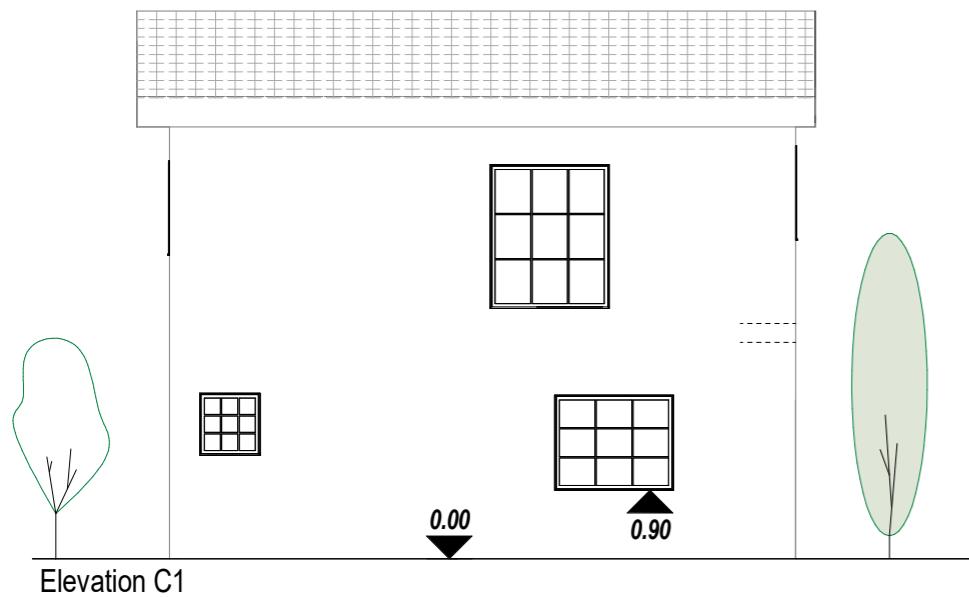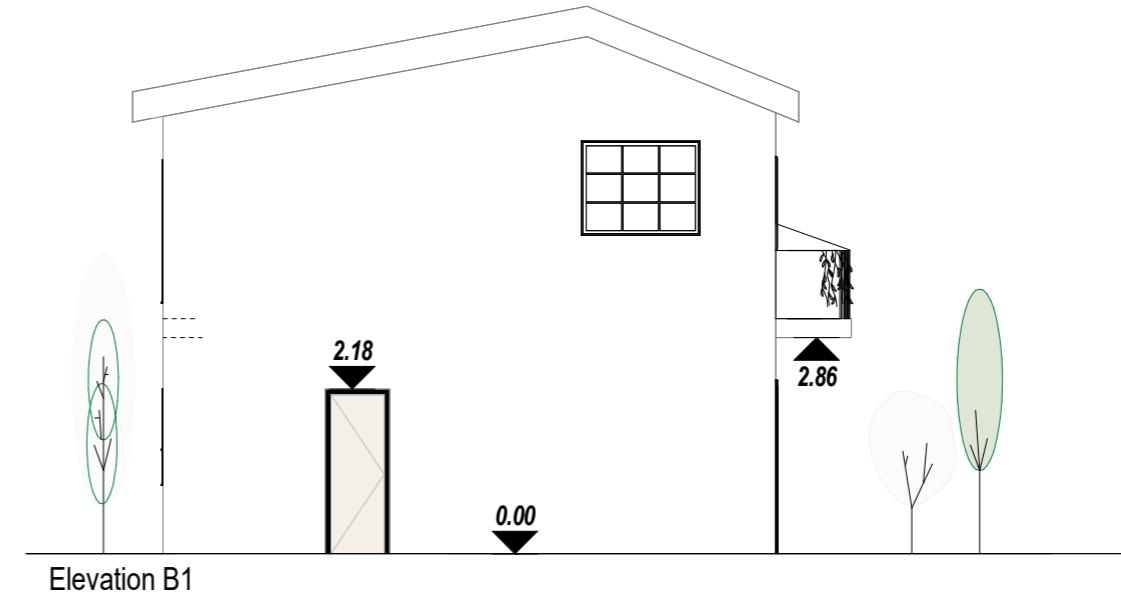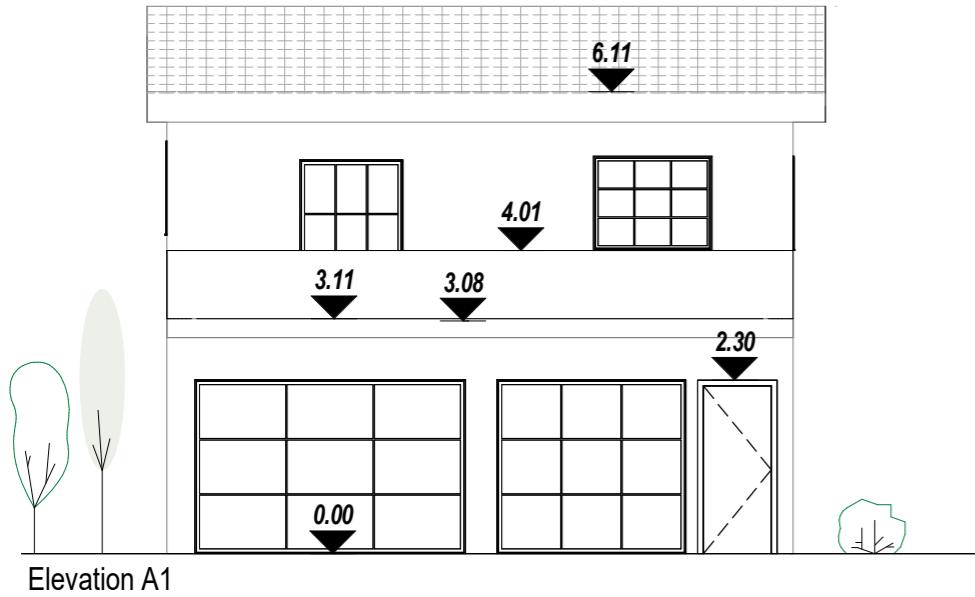

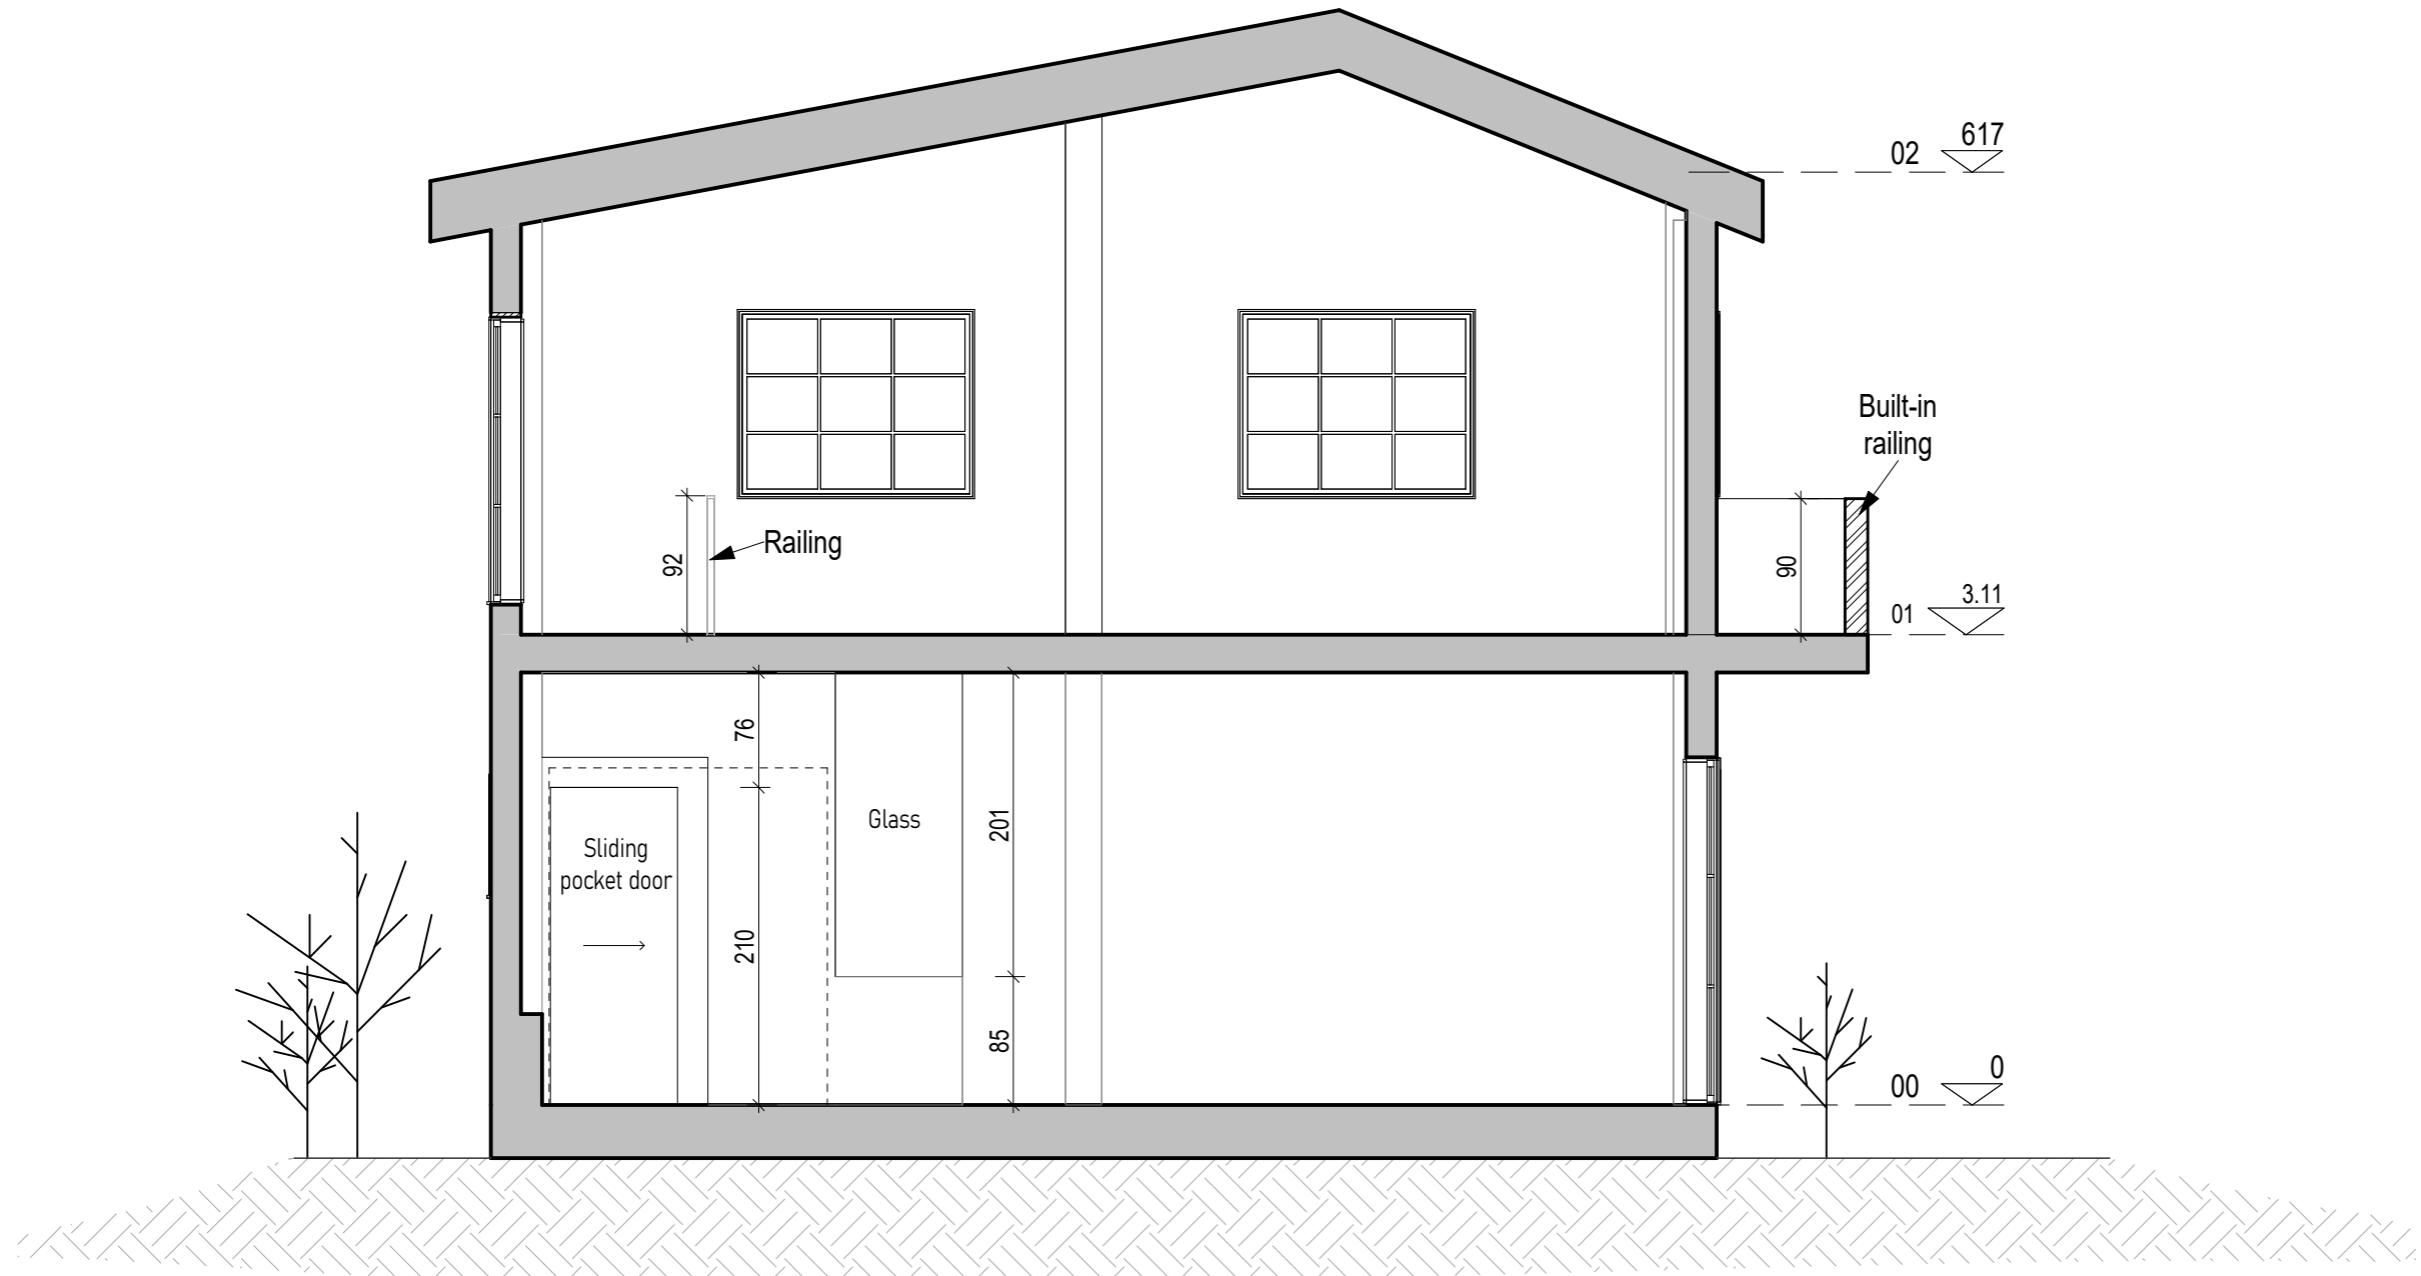

TH Architecture

972-542214335+ : 70

Client

Shai alfasi Matan morali

Project

k-pn restaurant

No

12

Scale

1 : 50

Date

03/12/2024 22:32:27



TH Architecture

972-542214335+ : 70

Client

Shai alfasi Matan morali

Project

k-pn restaurant

No


13


Scale

1 : 50

Date

03/12/2024 22:32:27

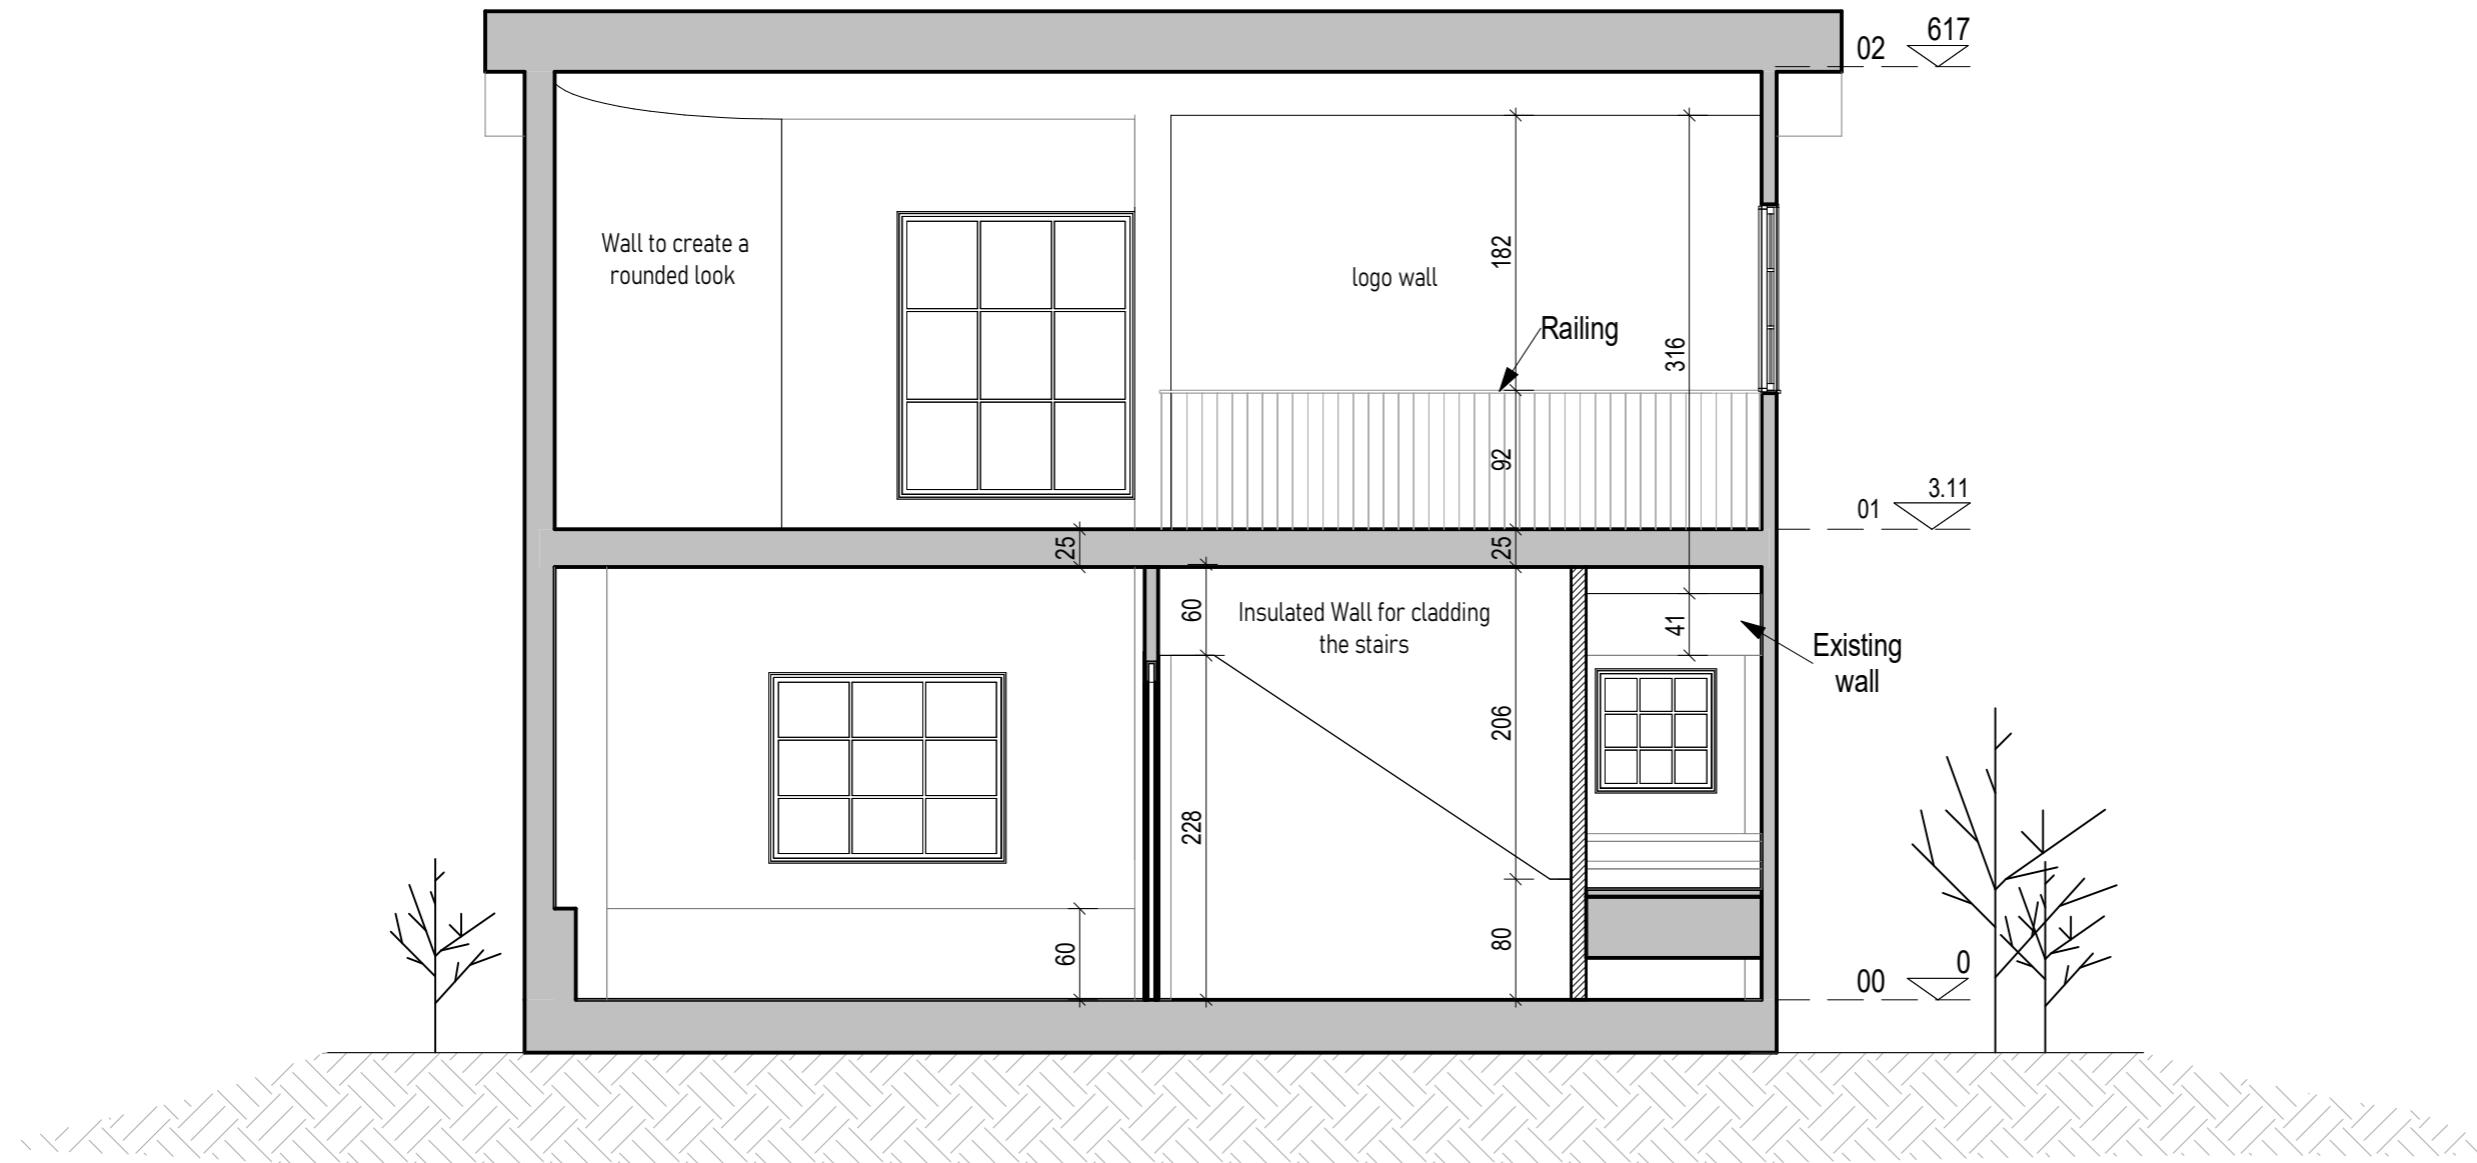

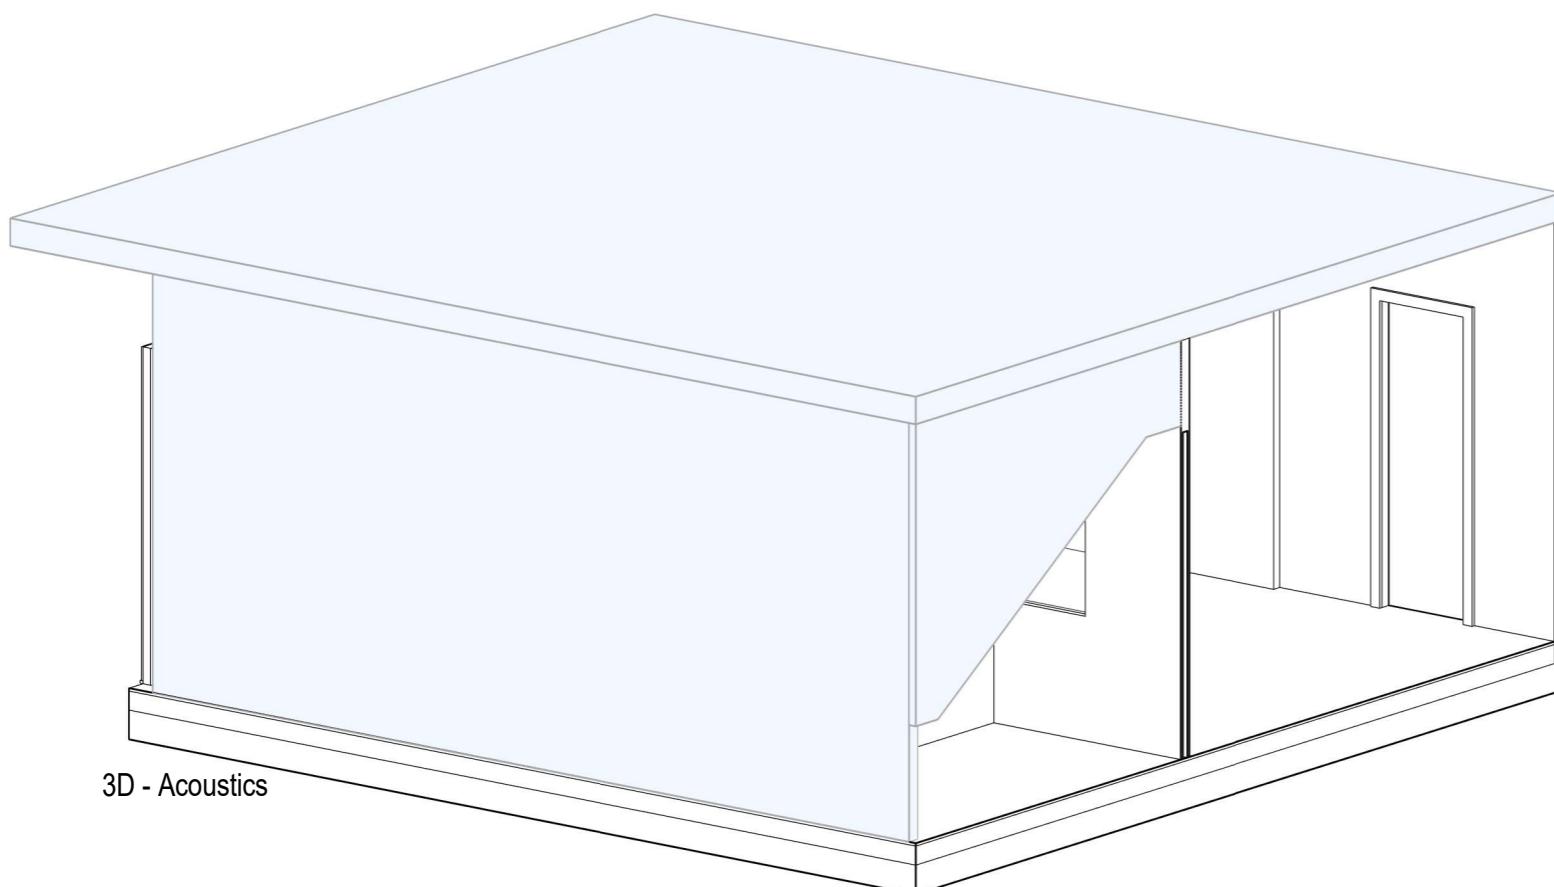



According to the need for acoustic insulation, elements that need to be insulated are marked in blue - 

Proposed solution for walls:

Insulation using acoustic insulation sheets – thin rubber surfaces provide very high-level acoustic insulation without taking up much space. They are suitable for use when space-saving is important, such as when adding insulation to an existing wall, or when there is a need to insulate against very loud noises.

Proposed solution for floor-to-floor insulation:

Add insulation under the flooring of the upper floor – after removing the existing flooring, acoustic sheets, felt, or any other acoustic insulation solution can be laid, followed by the installation of the new flooring.

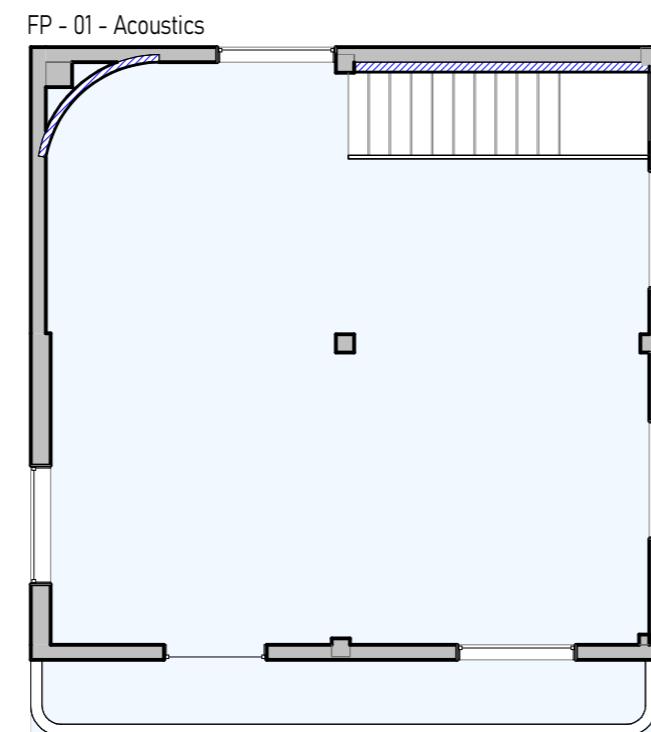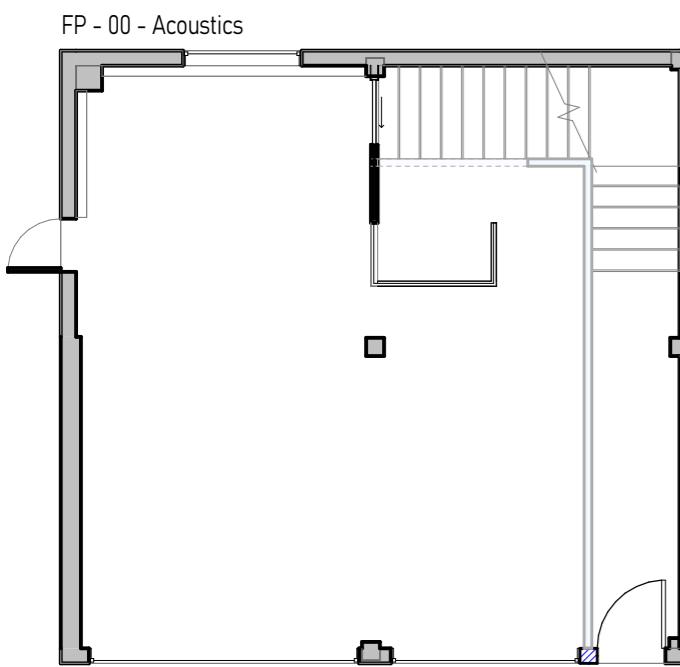

TH Architecture

972-542214335+ :נע

Client

Shai alfasi Matan morali

Project

k-pn restaurant

No

14

Scale

1 : 100

Date

03/12/2024 22:32:29



TH Architecture

972-542214335+ : 70

Client

Shai alfasi Matan morali

Project

k-pn restaurant

No


15

Scale


1 : 50

Date

03/12/2024 22:32:31

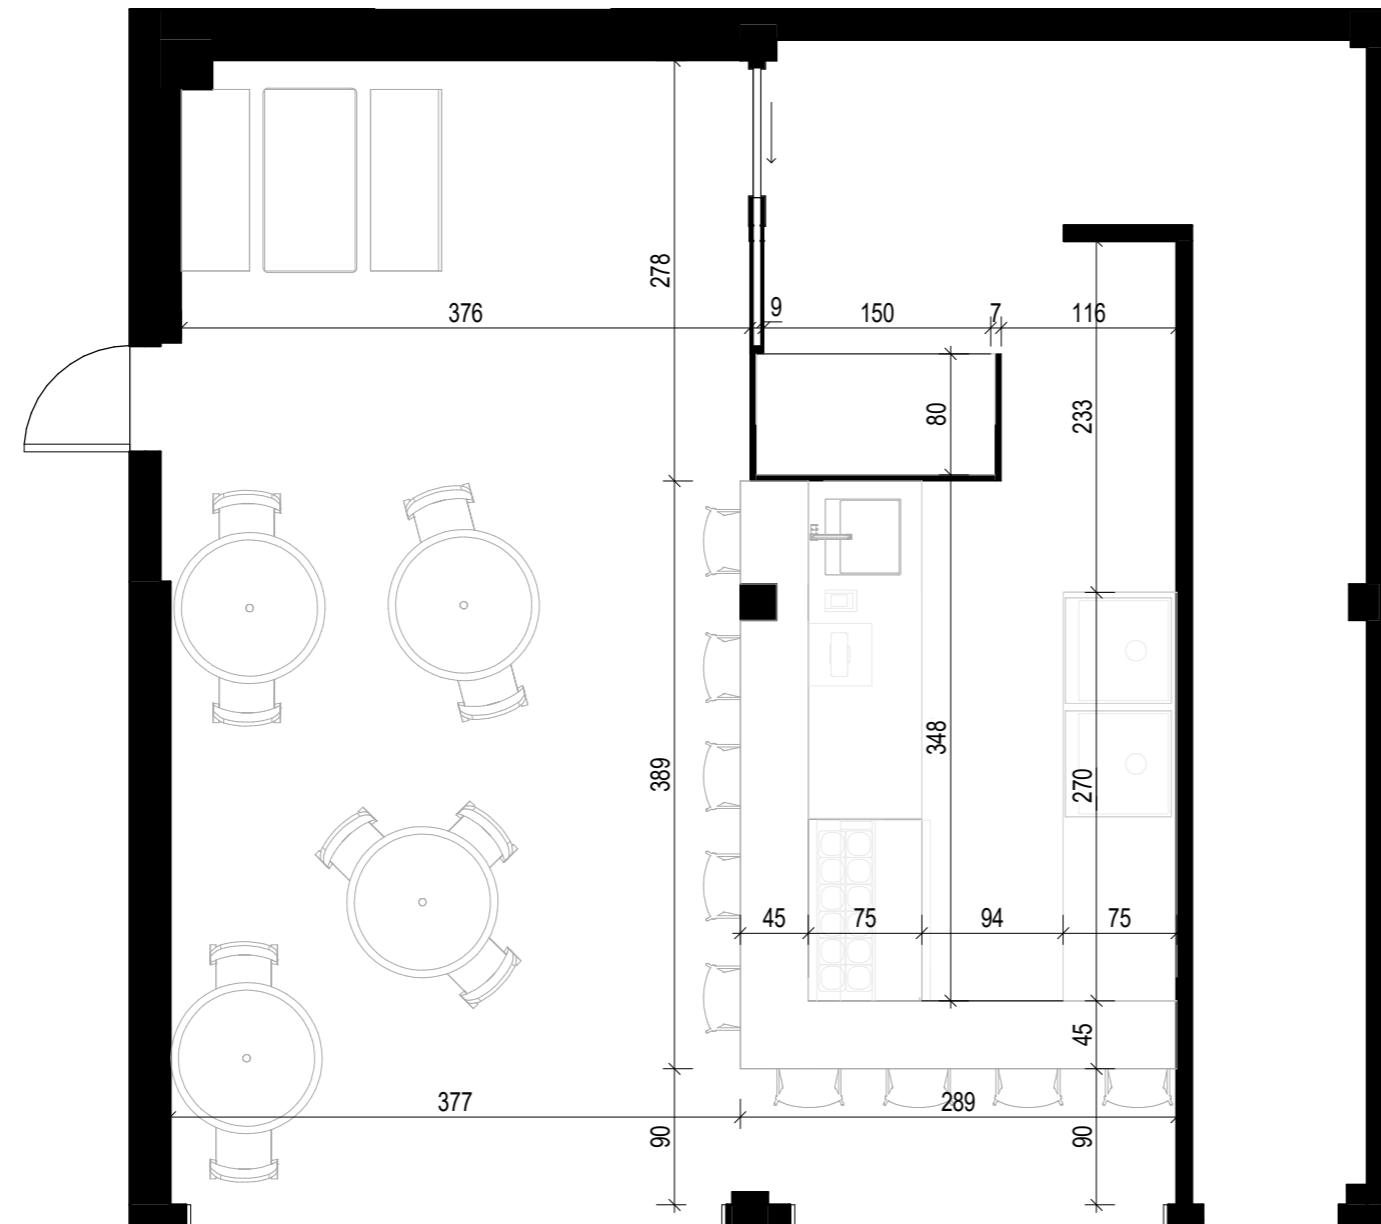**Note:**

In case of any discrepancies in measurements or for any custom-made products based on specific dimensions, it is imperative to take measurements directly from the site. Please note that the current design was not based on an existing measurement plan but rather on approximate field measurements. Therefore, final measurements must be verified on-site prior to manufacturing or installation.

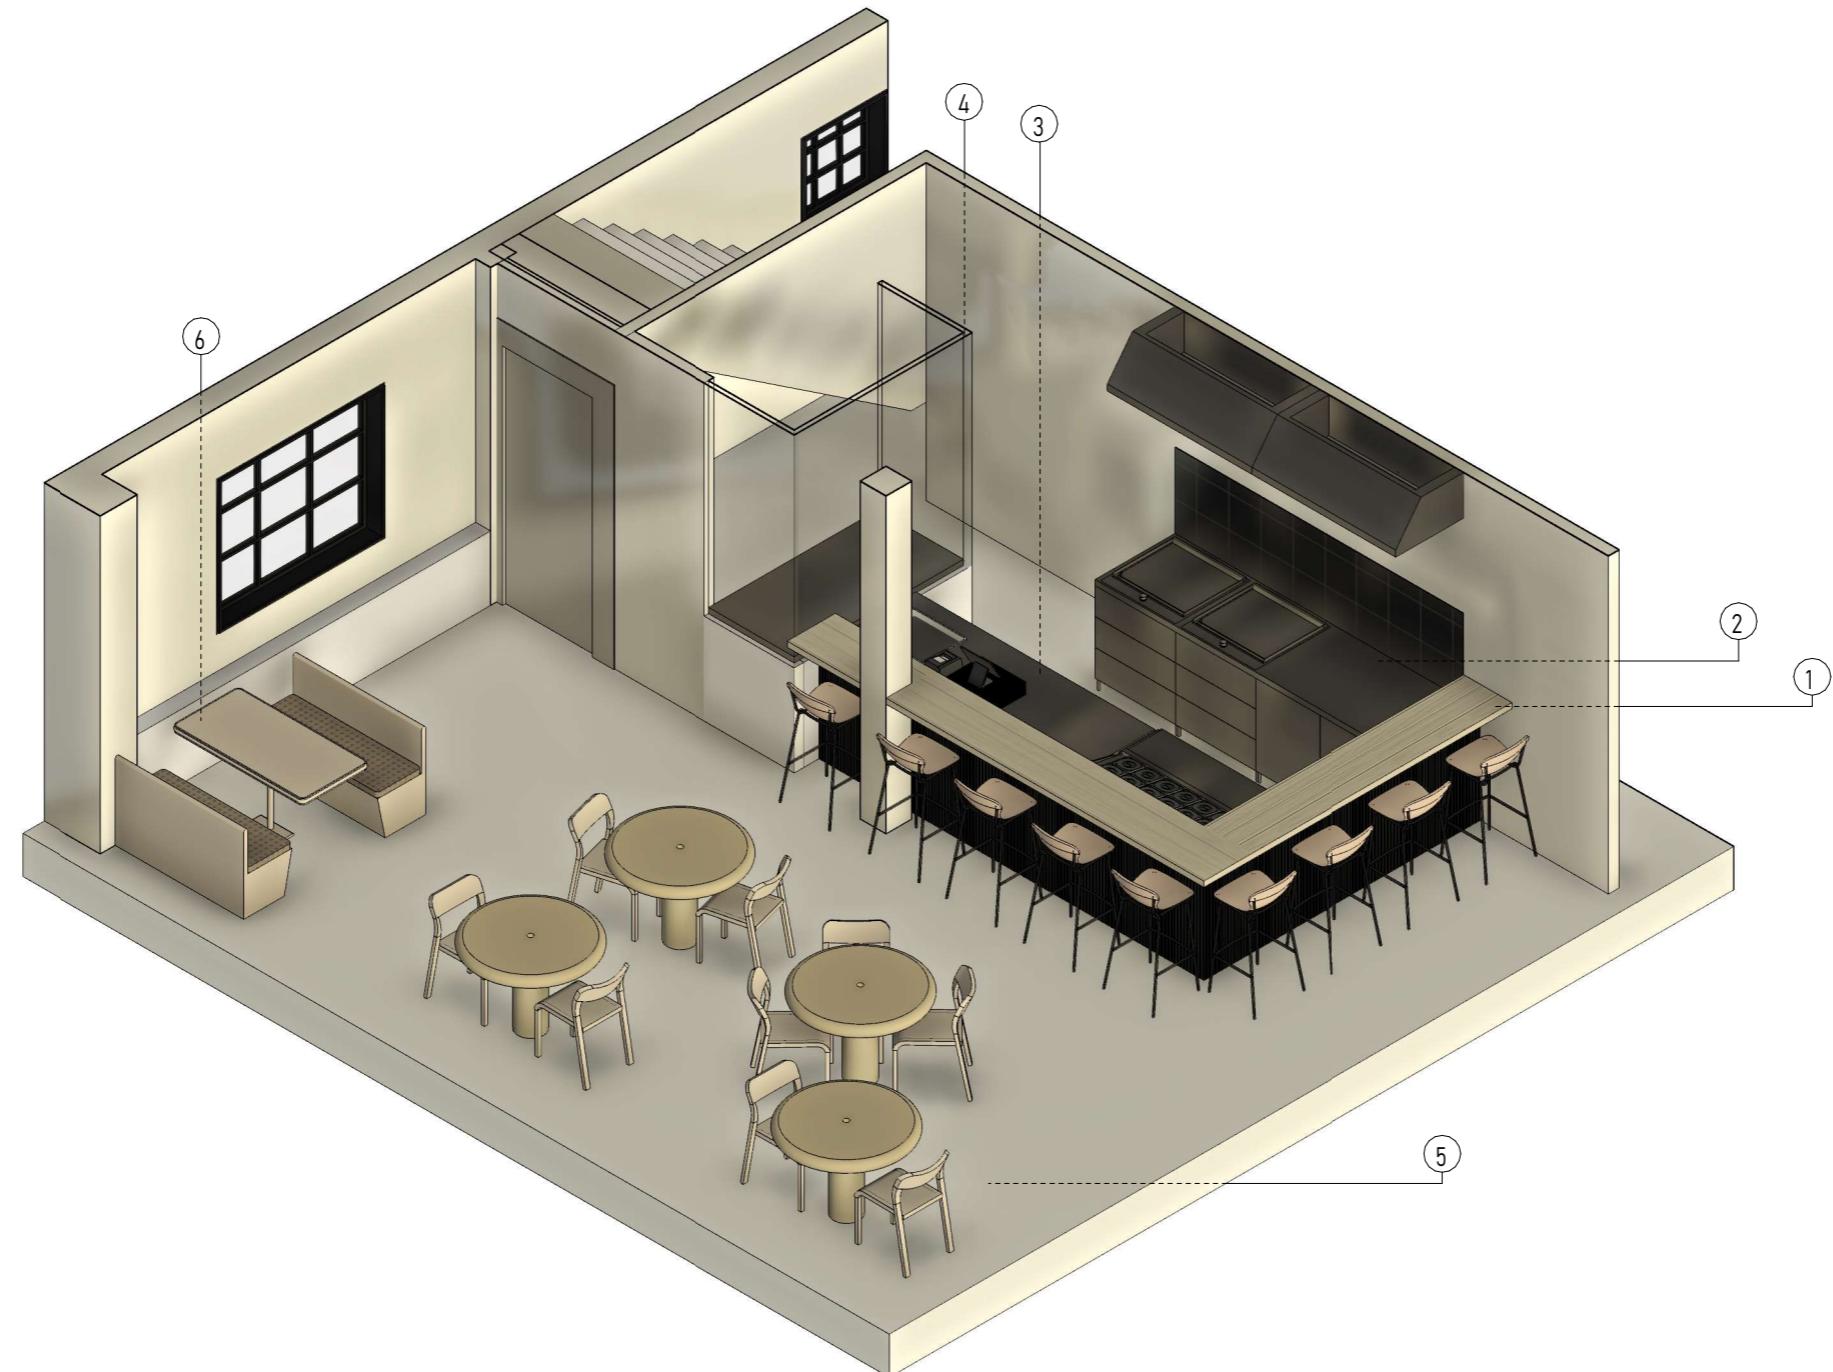

- ① Bar
- ② Warm work surface
- ③ Cold work surface
- ④ Aquarium - meat preparation area
- ⑤ Seating area
- ⑥ Group seating area



TH Architecture

972-542214335+ :נע

Client

Shai alfasi Matan morali

Project

k-pn restaurant

No

16

Scale

Date

03/12/2024 22:32:34



TH Architecture

972-542214335+ : 70

Client

Shai alfasi Matan morali

Project

k-pn restaurant

No







17



Scale

As indicated

Date

03/12/2024 22:32:37

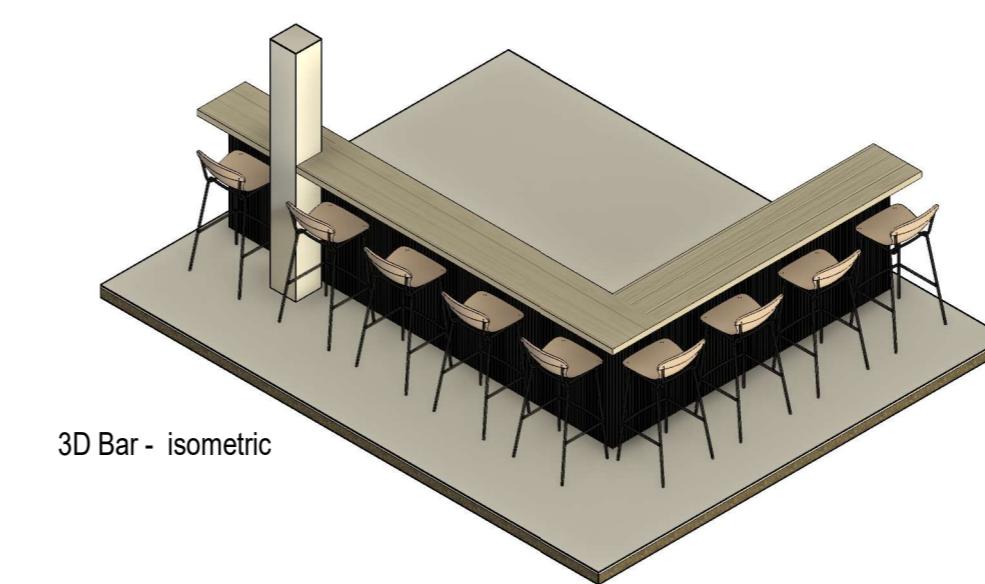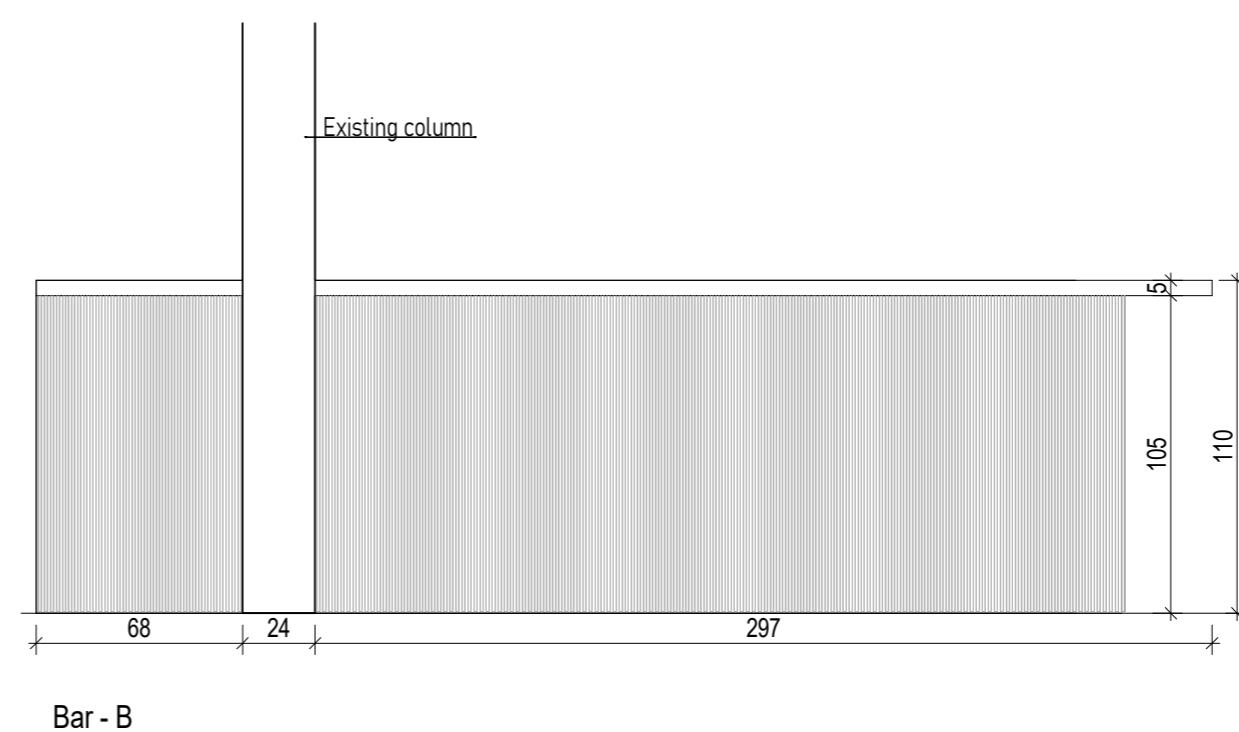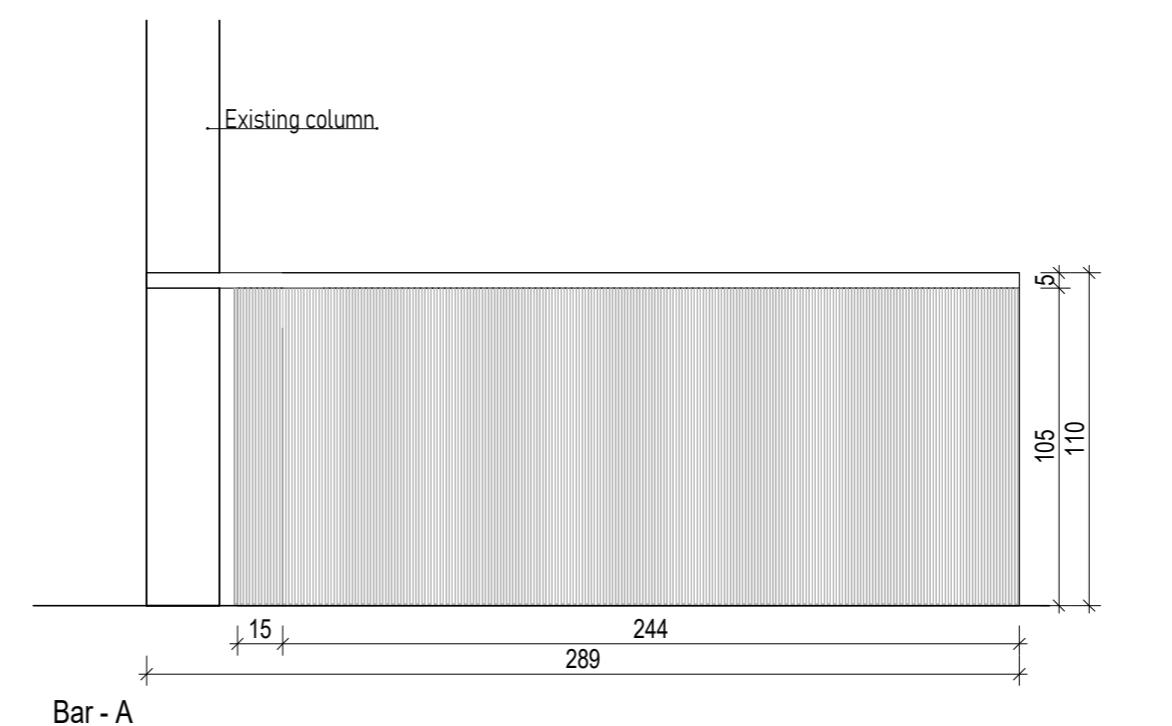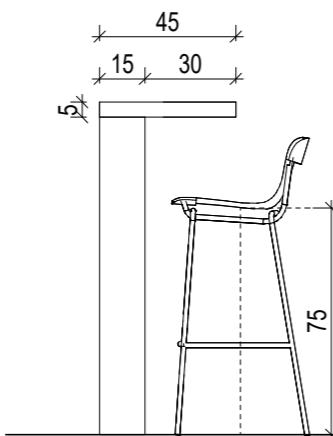
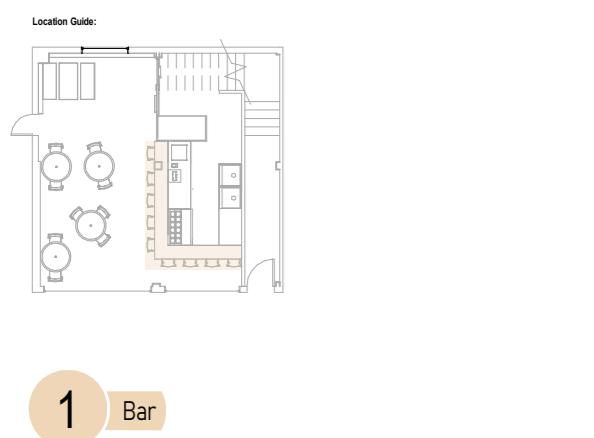
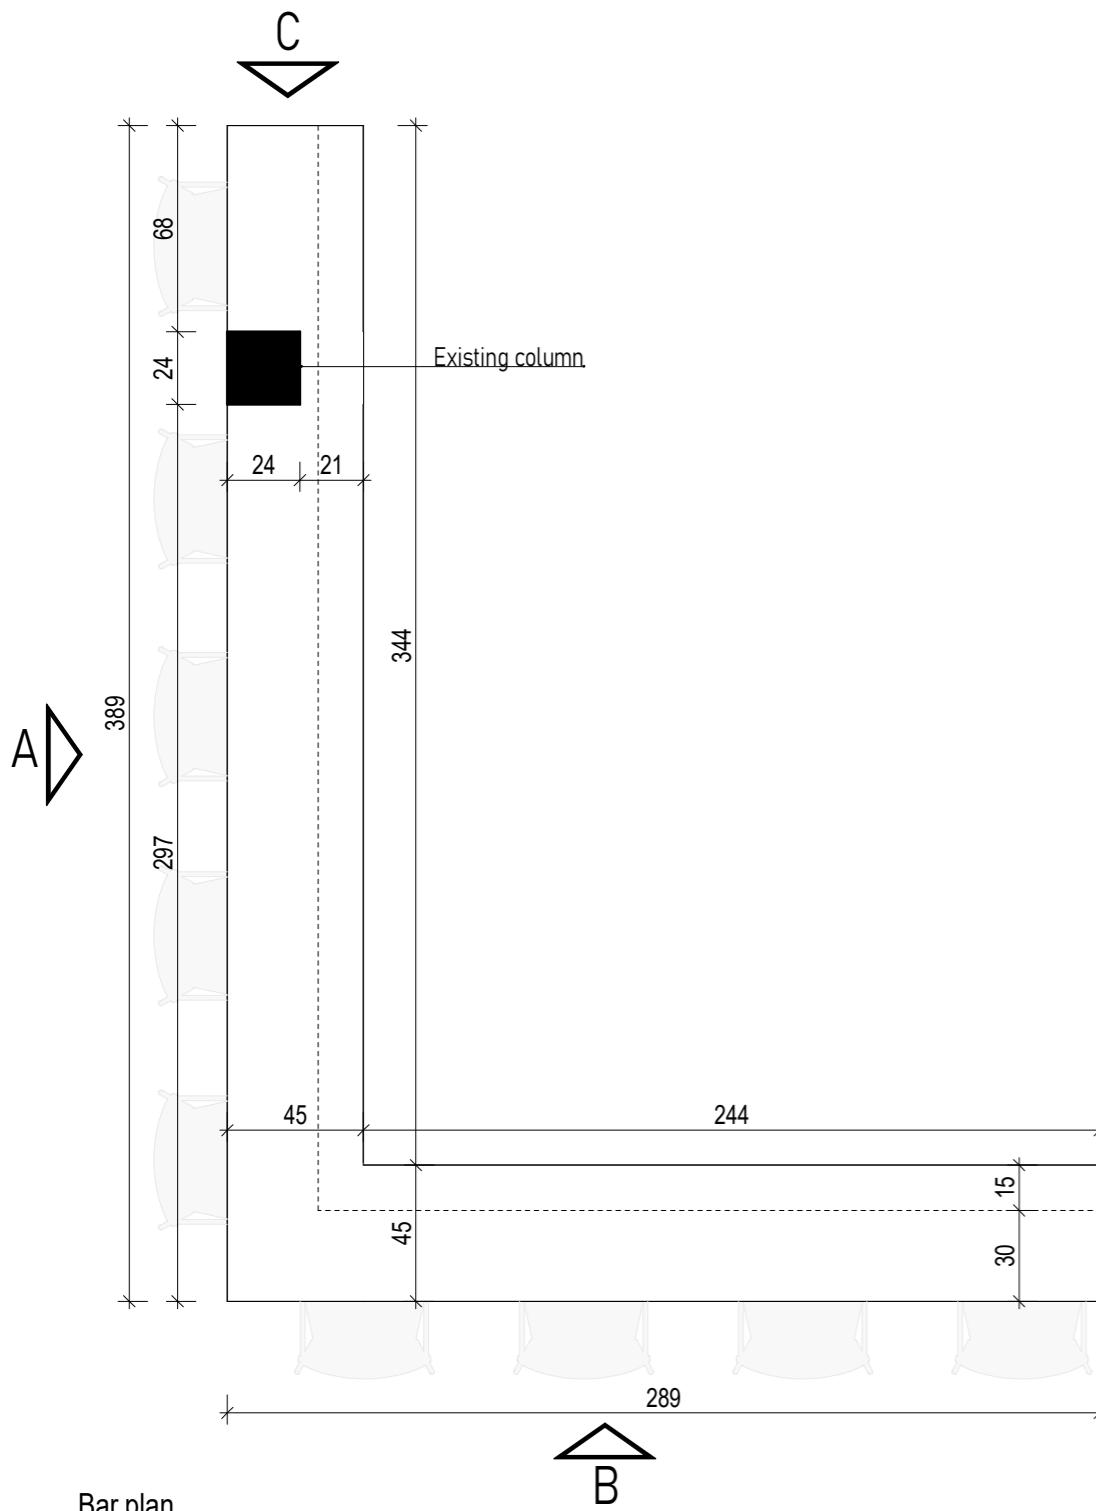


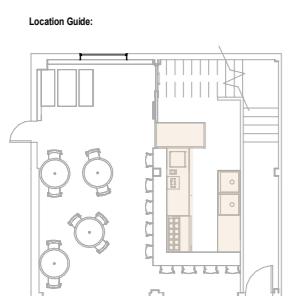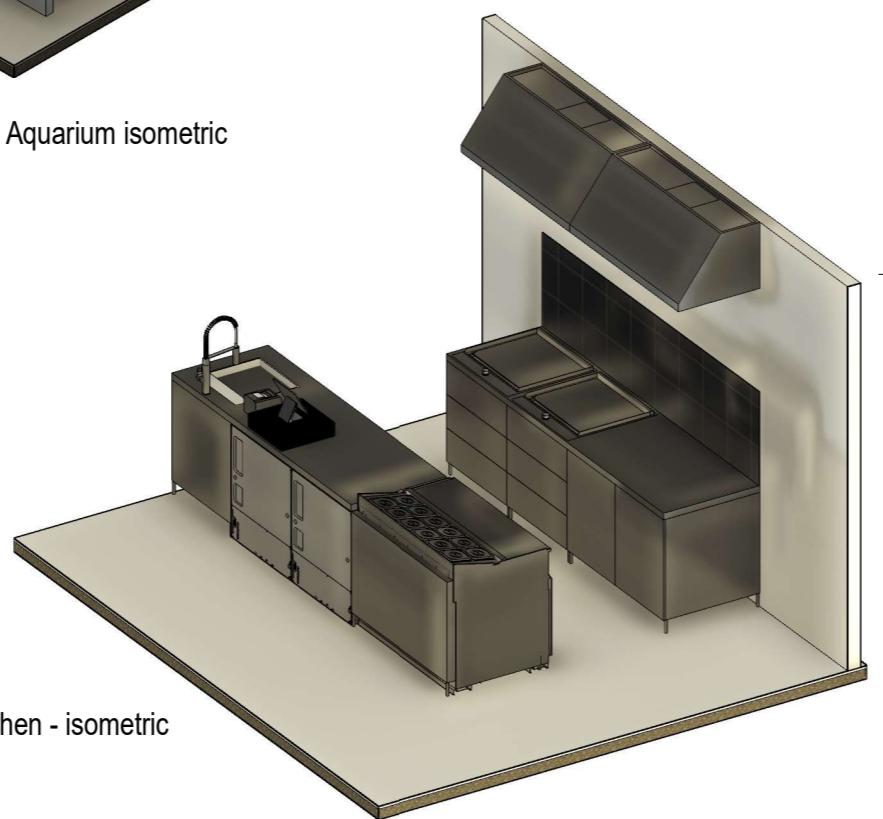

2 Warm work surface

3 Cold work surface

4 Aquarium - meat preparation area

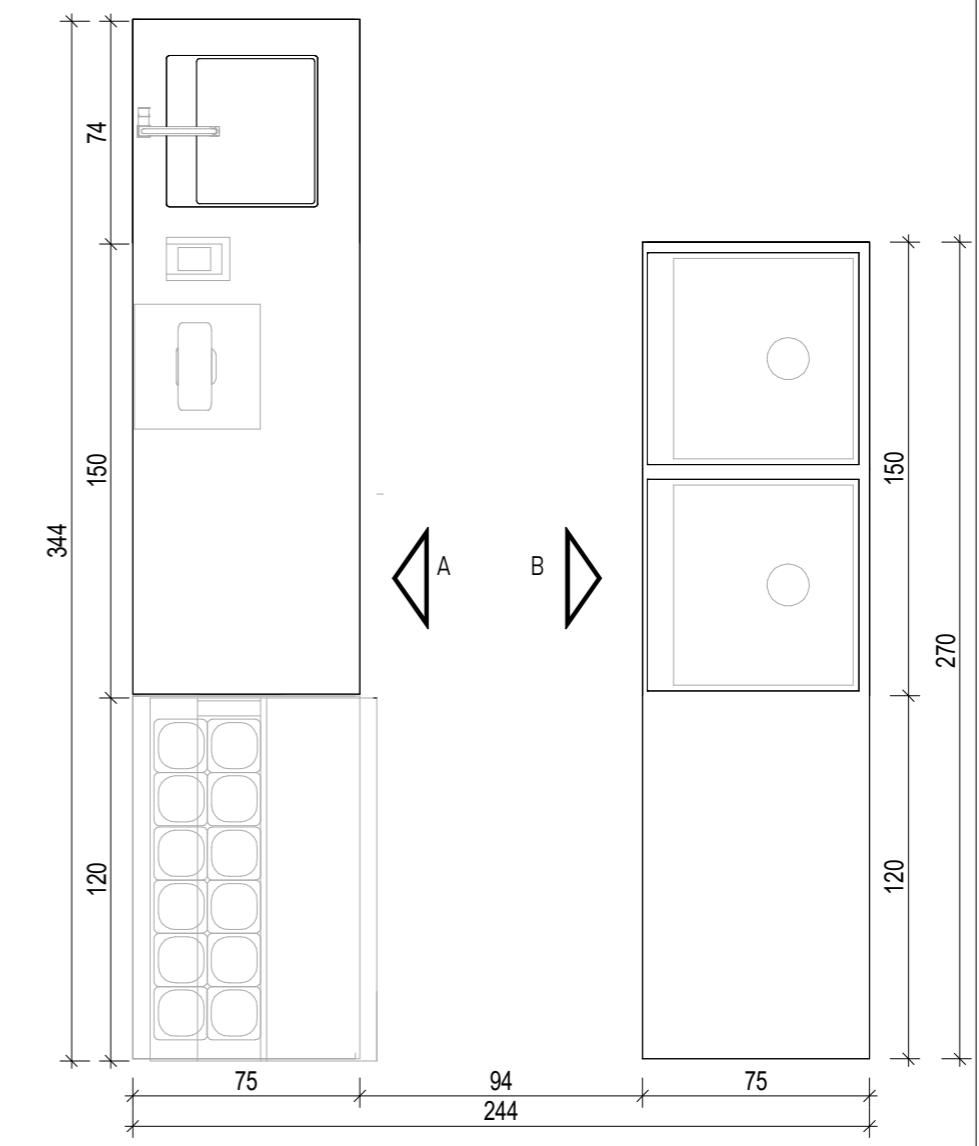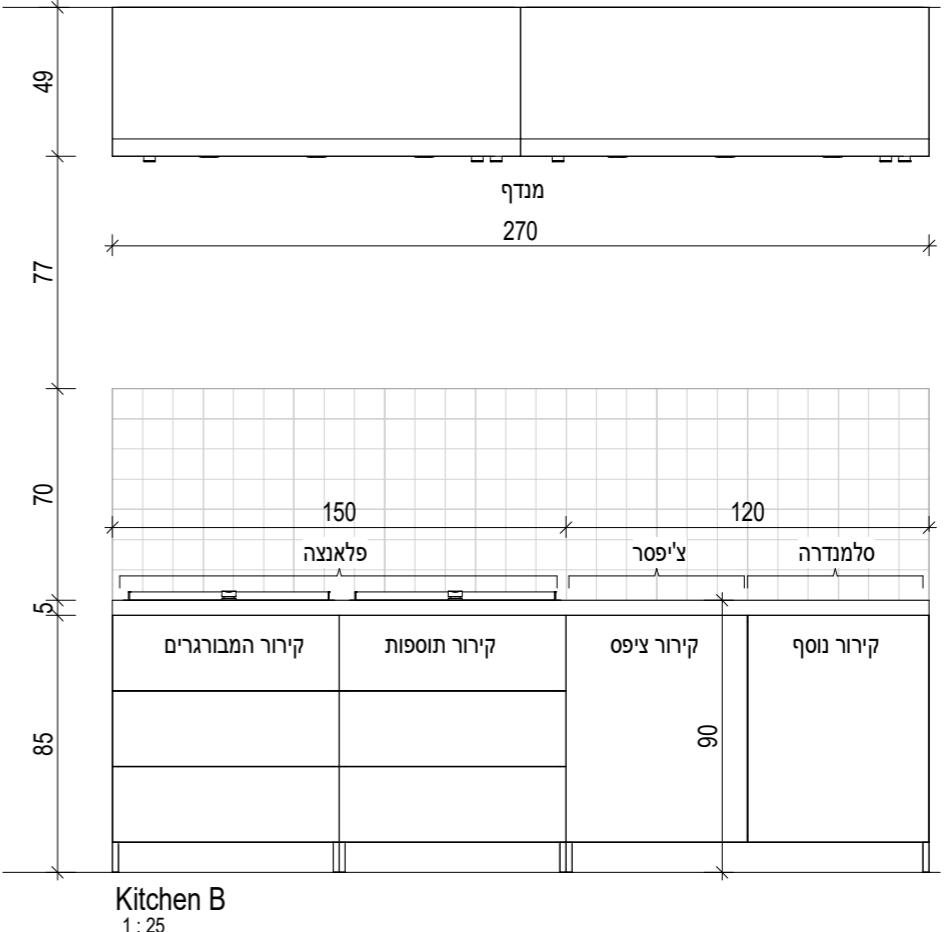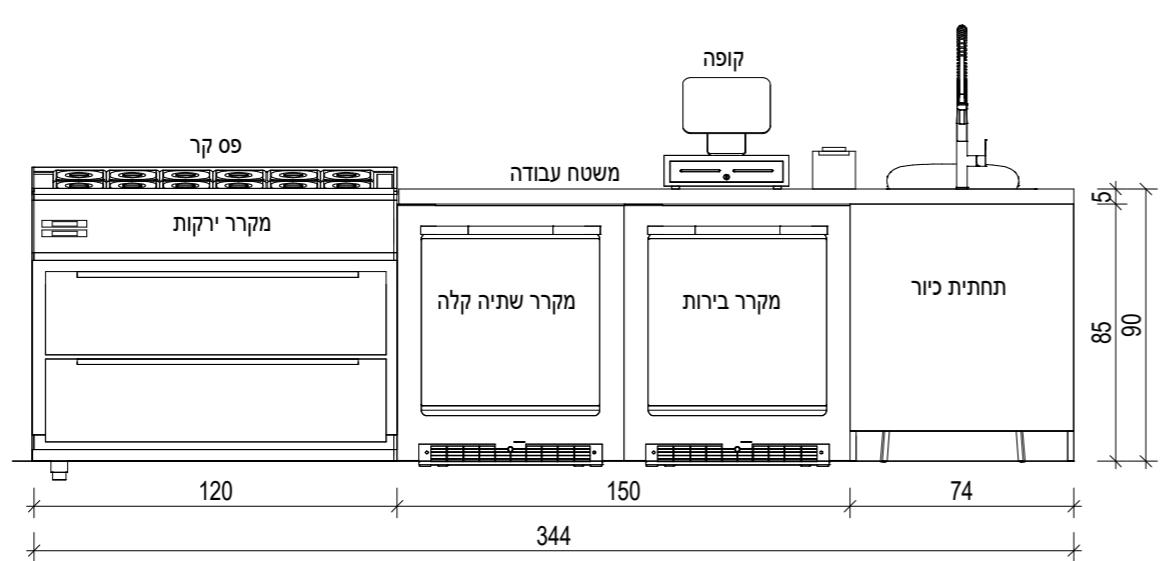

TH Architecture

טל': 972-542214335+

Client

Shai alfasi Matan morali

Project

k-pn restaurant

18

Scale

As indicated

Date

03/12/2024 22:32:45



TH Architecture

972-542214335+ : 70

Client

Shai alfasi Matan morali

Project

k-pn restaurant

No

19

Scale

1 : 100

Date

03/12/2024 22:32:46

הנורה	מיקום	פירוט	חומר
ציפוי עמיד לקרינת UV ולכתמים	רצפה	מיקרו טופיניג באימור מט באגון בז' נטראלי במרקם אחד	
	משטח בר, כסאות בר, משטח עליון של בליטות קימות	עץ אלון מלא באימור שמן לעץ בצבע חום כהה באגון חם ובקטן טבעי	
	קירות	לבני חימר/בטון קל באימור טבעי וags בצבע בז' בהיר חם, מחוספס ולא אחיד	
	דלתות בר	קרמיקה באימור מט או חצי מבריק בצבע ירוק זית עם ריאציות קלות באגון. 6/20	
	ספה	עור/דמוי עור באימור מט עם טקסטורת עור טבעי בצבע שחור	
	קיר	פלטות עץ MDF באימור מט באגון אגוז כהה	
	קירות	טיח מינרלי באגוני לבן בז' ושמנת בקטן טבעי, באימור מט גולמי	
	קיר פס חם	קרמיקה באימור מבריק בצבע לבן עם רובה שחורה 15/15	



TH Architecture

טל': 972-542214335+

Client

Shai alfasi Matan morali

Project

k-pn restaurant

No

20

Scale

1 : 100

Date

03/12/2024 22:32:48

הערה

מיקום

פירוט

חומר

	פס רגליים לבר	מתכת (פלדה) בציפוי ברונזה כהה, קוורט צינור 4 ס"מ	
	ריהוט	עכ מלא/mdf מצופה פורניר גימור מט טבעי בגוון אגוז	
	ריהוט	ריפוד דמוי עור בגוון חום בגימור תפרים אסימ	
	ריהוט	עכ מלא בגוון אגוז בגימור שמן עכ בגוון טבעי	
	קיר	גוף תאורה מתכת פלדה/אלומיניום שחור בגימור מבריק	
	קיר	גוף תאורה מתכת פלדה/אלומיניום שחור בגימור מט	
	תקרה	גוף תאורה מתכת פלדה/אלומיניום שחור בגימור מט	
	מתלה תמונה	שרשראות ברזל	



TH Architecture

טל': 972-542214335+

Client

Shai alfasi Matan morali

Project

k-pn restaurant

No

21

Scale

1 : 100

Date

03/12/2024 22:32:49

הערה	מקום	פירוט	חומר
	תקרה מעל הבר	חומר מתכתagimor שחור מט	
	קיר	חומר מתכת אלומיניוםagimor שחור מט	
		עץ זית בגובה של כ. 1.5 מטרים כד עשוי חרס	
	דלת כניסה למטבח	דלת הזזה מעק מלא (עץ תעשייתי עם גימור כהה) ציפוי לכה או צבע כהה להאגנה ועמידות בסגנון כפרי/תעשייתי	
	דלת הזזה	ידית מתכת ארוכהagimor פלייז מוברש מלדה או אלומיניום	
	תחתיות בר ותקרת אקווריום	תאורת לד שקוועת תקרה	



TH Architecture

טל': 972-542214335+

Client

Shai alfasi Matan morali

Project

k-pn restaurant

No

22

Scale

1 : 100

Date

03/12/2024 22:32:50



TH Architecture

972-542214335+ : 70

Client

Shai alfasi Matan morali

Project

k-pn restaurant

No

23

Scale

Date

03/12/2024 22:32:54





TH Architecture

972-542214335+ : 70

Client

Shai alfasi Matan morali

Project

k-pn restaurant

No


24

Scale

1 : 100

Date

03/12/2024 22:33:05

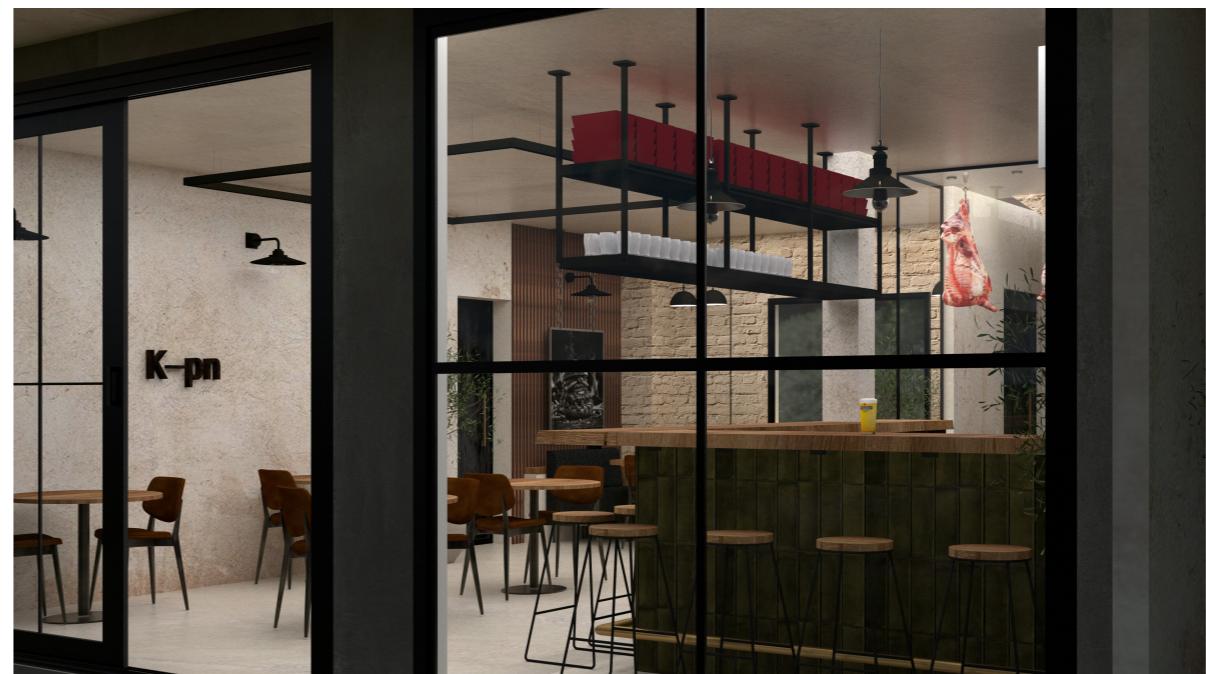



TH Architecture

972-542214335+ : 70

Client

Shai alfasi Matan morali

Project

k-pn restaurant

No

25

Scale



Date

03/12/2024 22:33:10